



ZAPATA TÍPICA - DESARROLLOS ESTRUCTURALES

ESCALA:1/25

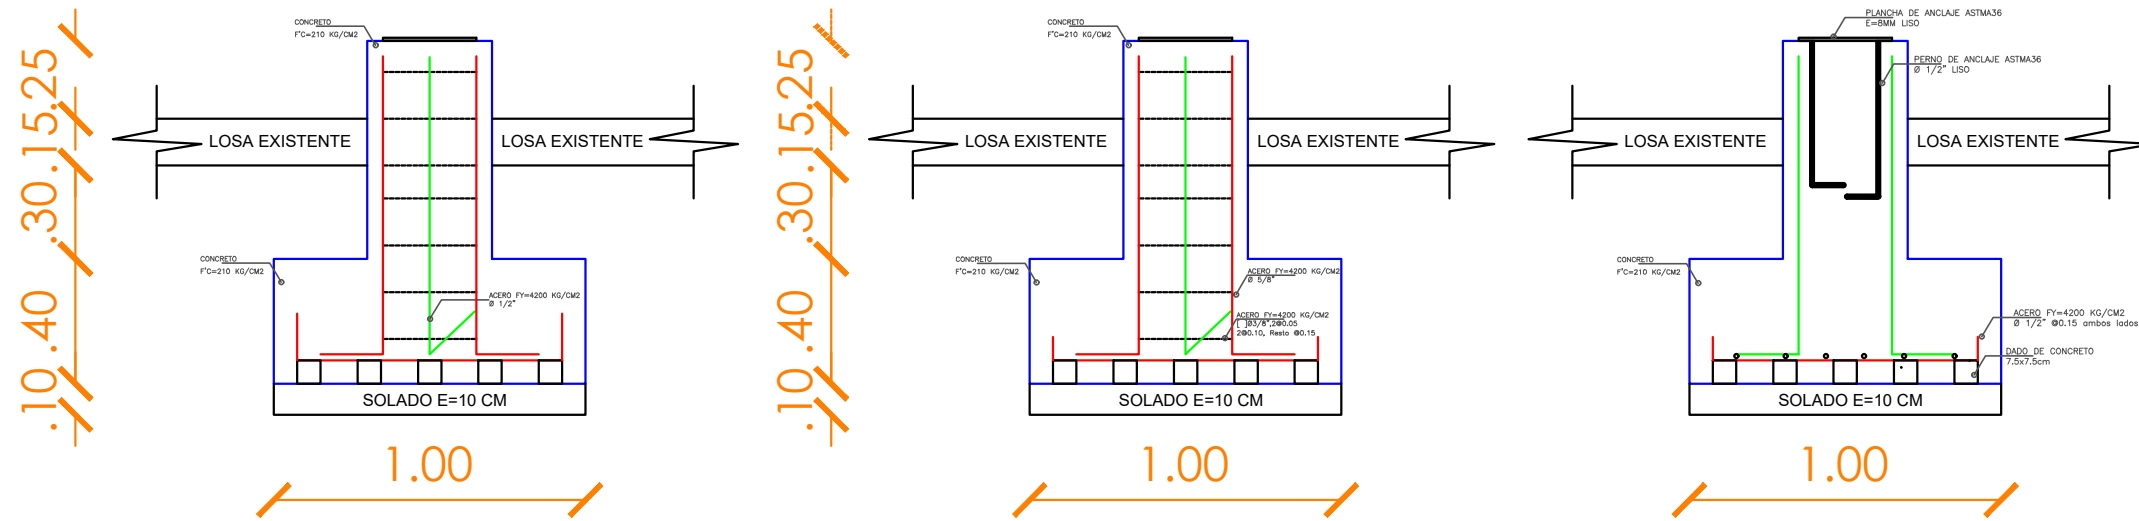


CUADRO DE ZAPATAS

ESCALA:1/25

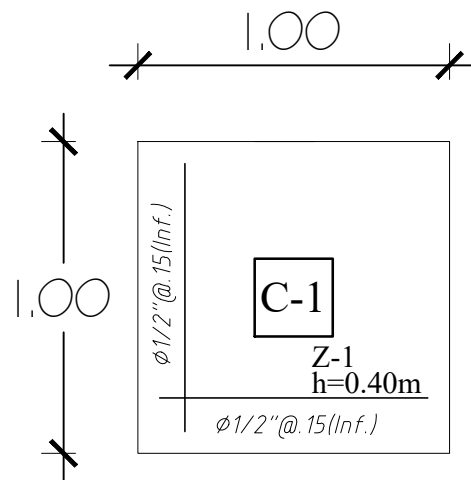

CUADRO DE COLUMNAS

ESCALA:1/25

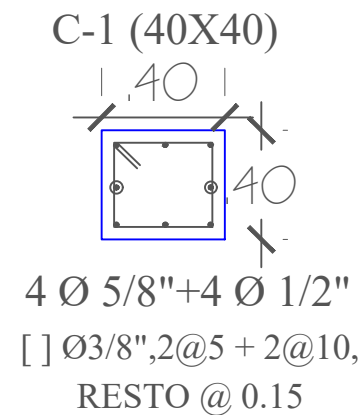

BASE TANQUE ALMACENAMIENTO DE AGUA A TEMP: 40°C

ZONA CALDERAS - CHI

A	DIC 2024	EMITIDO PARA APROBACION DEL CLIENTE	J.A.M.	
REV.	FECHA	DESCRIPCION DE REVISION	REVISADO	APROBADO

DISEÑADO POR:	—	FECHA:	ENERO 2025
DIBUJADO POR:	A.G.M.	FECHA:	ENERO 2025
REVISADO POR:	J.A.M.	FECHA:	ENERO 2025
APROBADO POR:		FECHA:	ENERO 2025



CLIENTE:	AUSTRAL GROUP S.A.A. PLANTA COISHCO
----------	--

TITULO: AUSTRAL – PLANTA DE HARINA
TANQUE DE ALMACENAMIENTO DE AGUA
BASE DE TANQUE – ZONA DE CALDEROS CHI

FORMATO	ESC.	PLANO N.º	REV:
A3	S/E	AU-PL-COI-ENER-P09	A