


TANQUE DESAIREADOR

ISOMÉTRICO - LINEAS DE VAPOR, AGUA BLANDA Y AGUA DE REPOSICIÓN

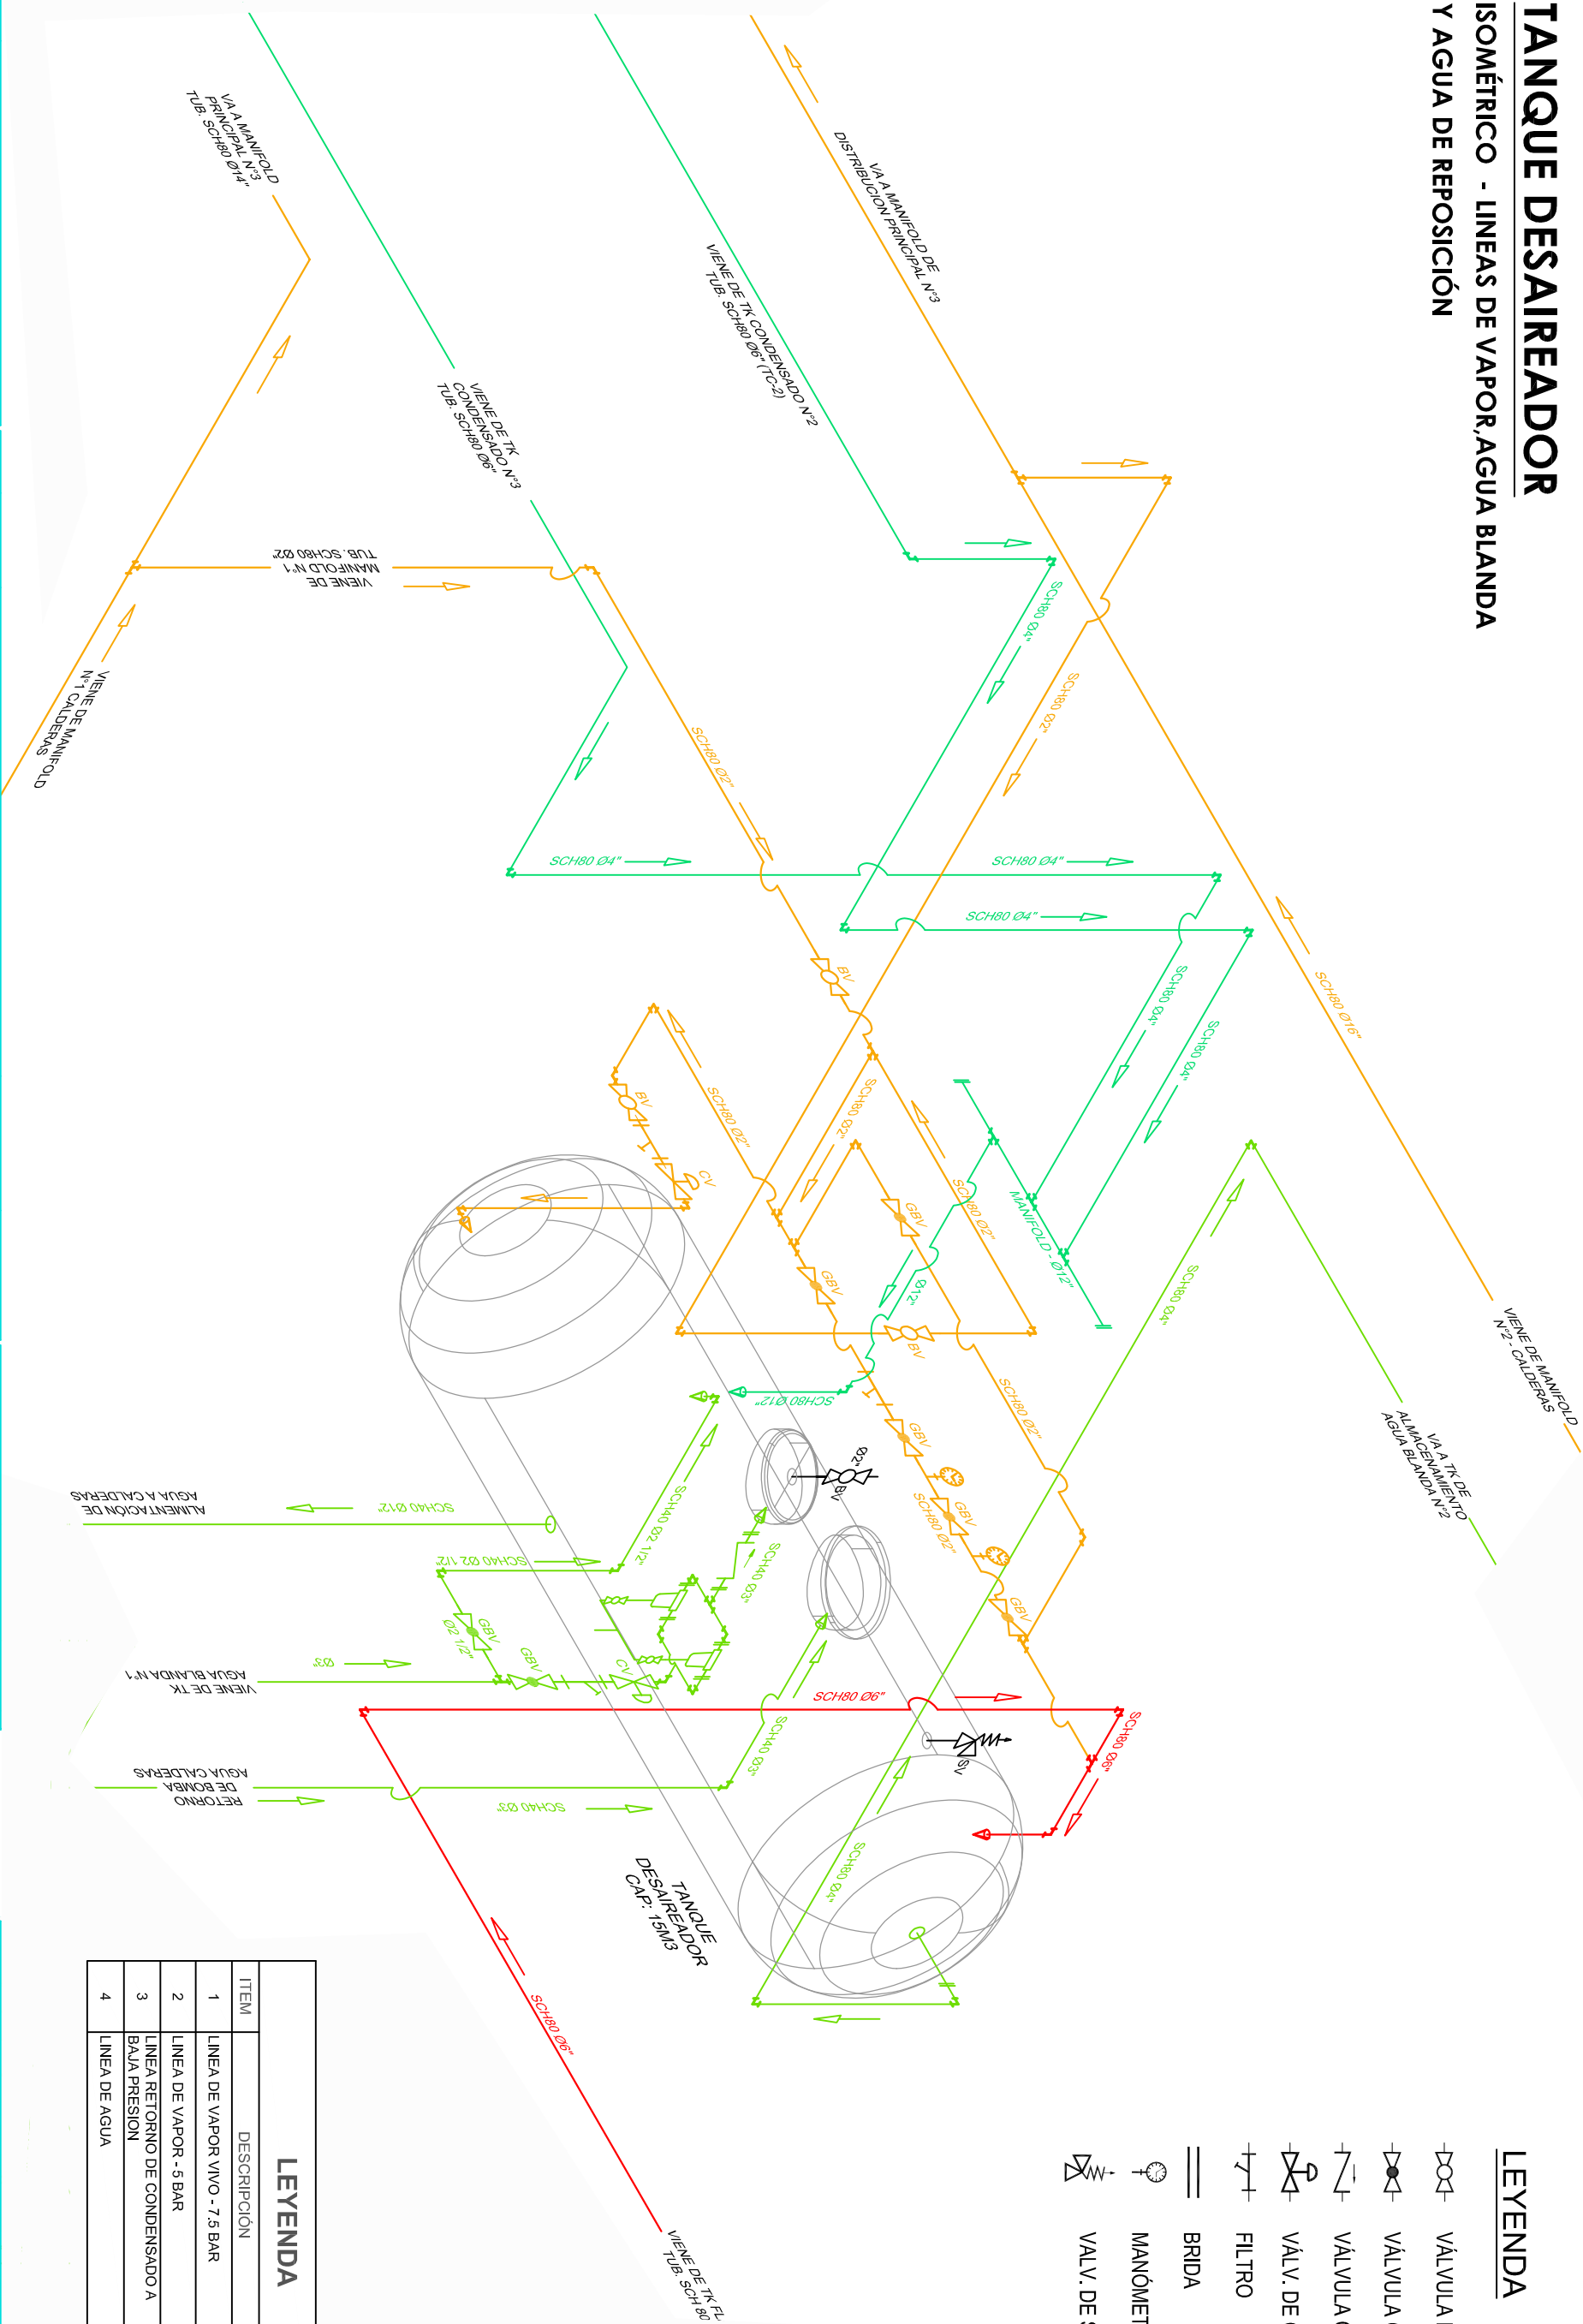

- ### LEYENDA
- Válvula BOLA (BV)
 - Válvula GLOBO (GBV)
 - Válvula CHECK (CHV)
 - Válv. DE CONTROL (CV)
 - BRIDA
 - MANÓMETRO
 - VALV. DE SEGURIDAD (SV)

LEYENDA		
ITEM	DESCRIPCION	SIMBOLO
1	LINEA DE VAPOR VIVO - 7.5 BAR	
2	LINEA DE VAPOR - 5 BAR	
3	LINEA RETORNO DE CONDENSADO A BAJA PRESION	
4	LINEA DE AGUA	

CLIENTE: AUSTRAL GROUP S.A.A. PLANTA COISHCO											
TITULO: AUSTRAL – PLANTA DE HARINA PLANO ISOMETRICO LINEAS DE VAPOR, AGUA BLANDA Y AGUA DE REPOSICION PARA TK DESAREADOR											
FORMATO A3 ESQ. S/C PLANO N.º AU-COI-VAPOR-P07 REV: A											
1 2 3 4 5 6 7 8 9 10 11 12											