


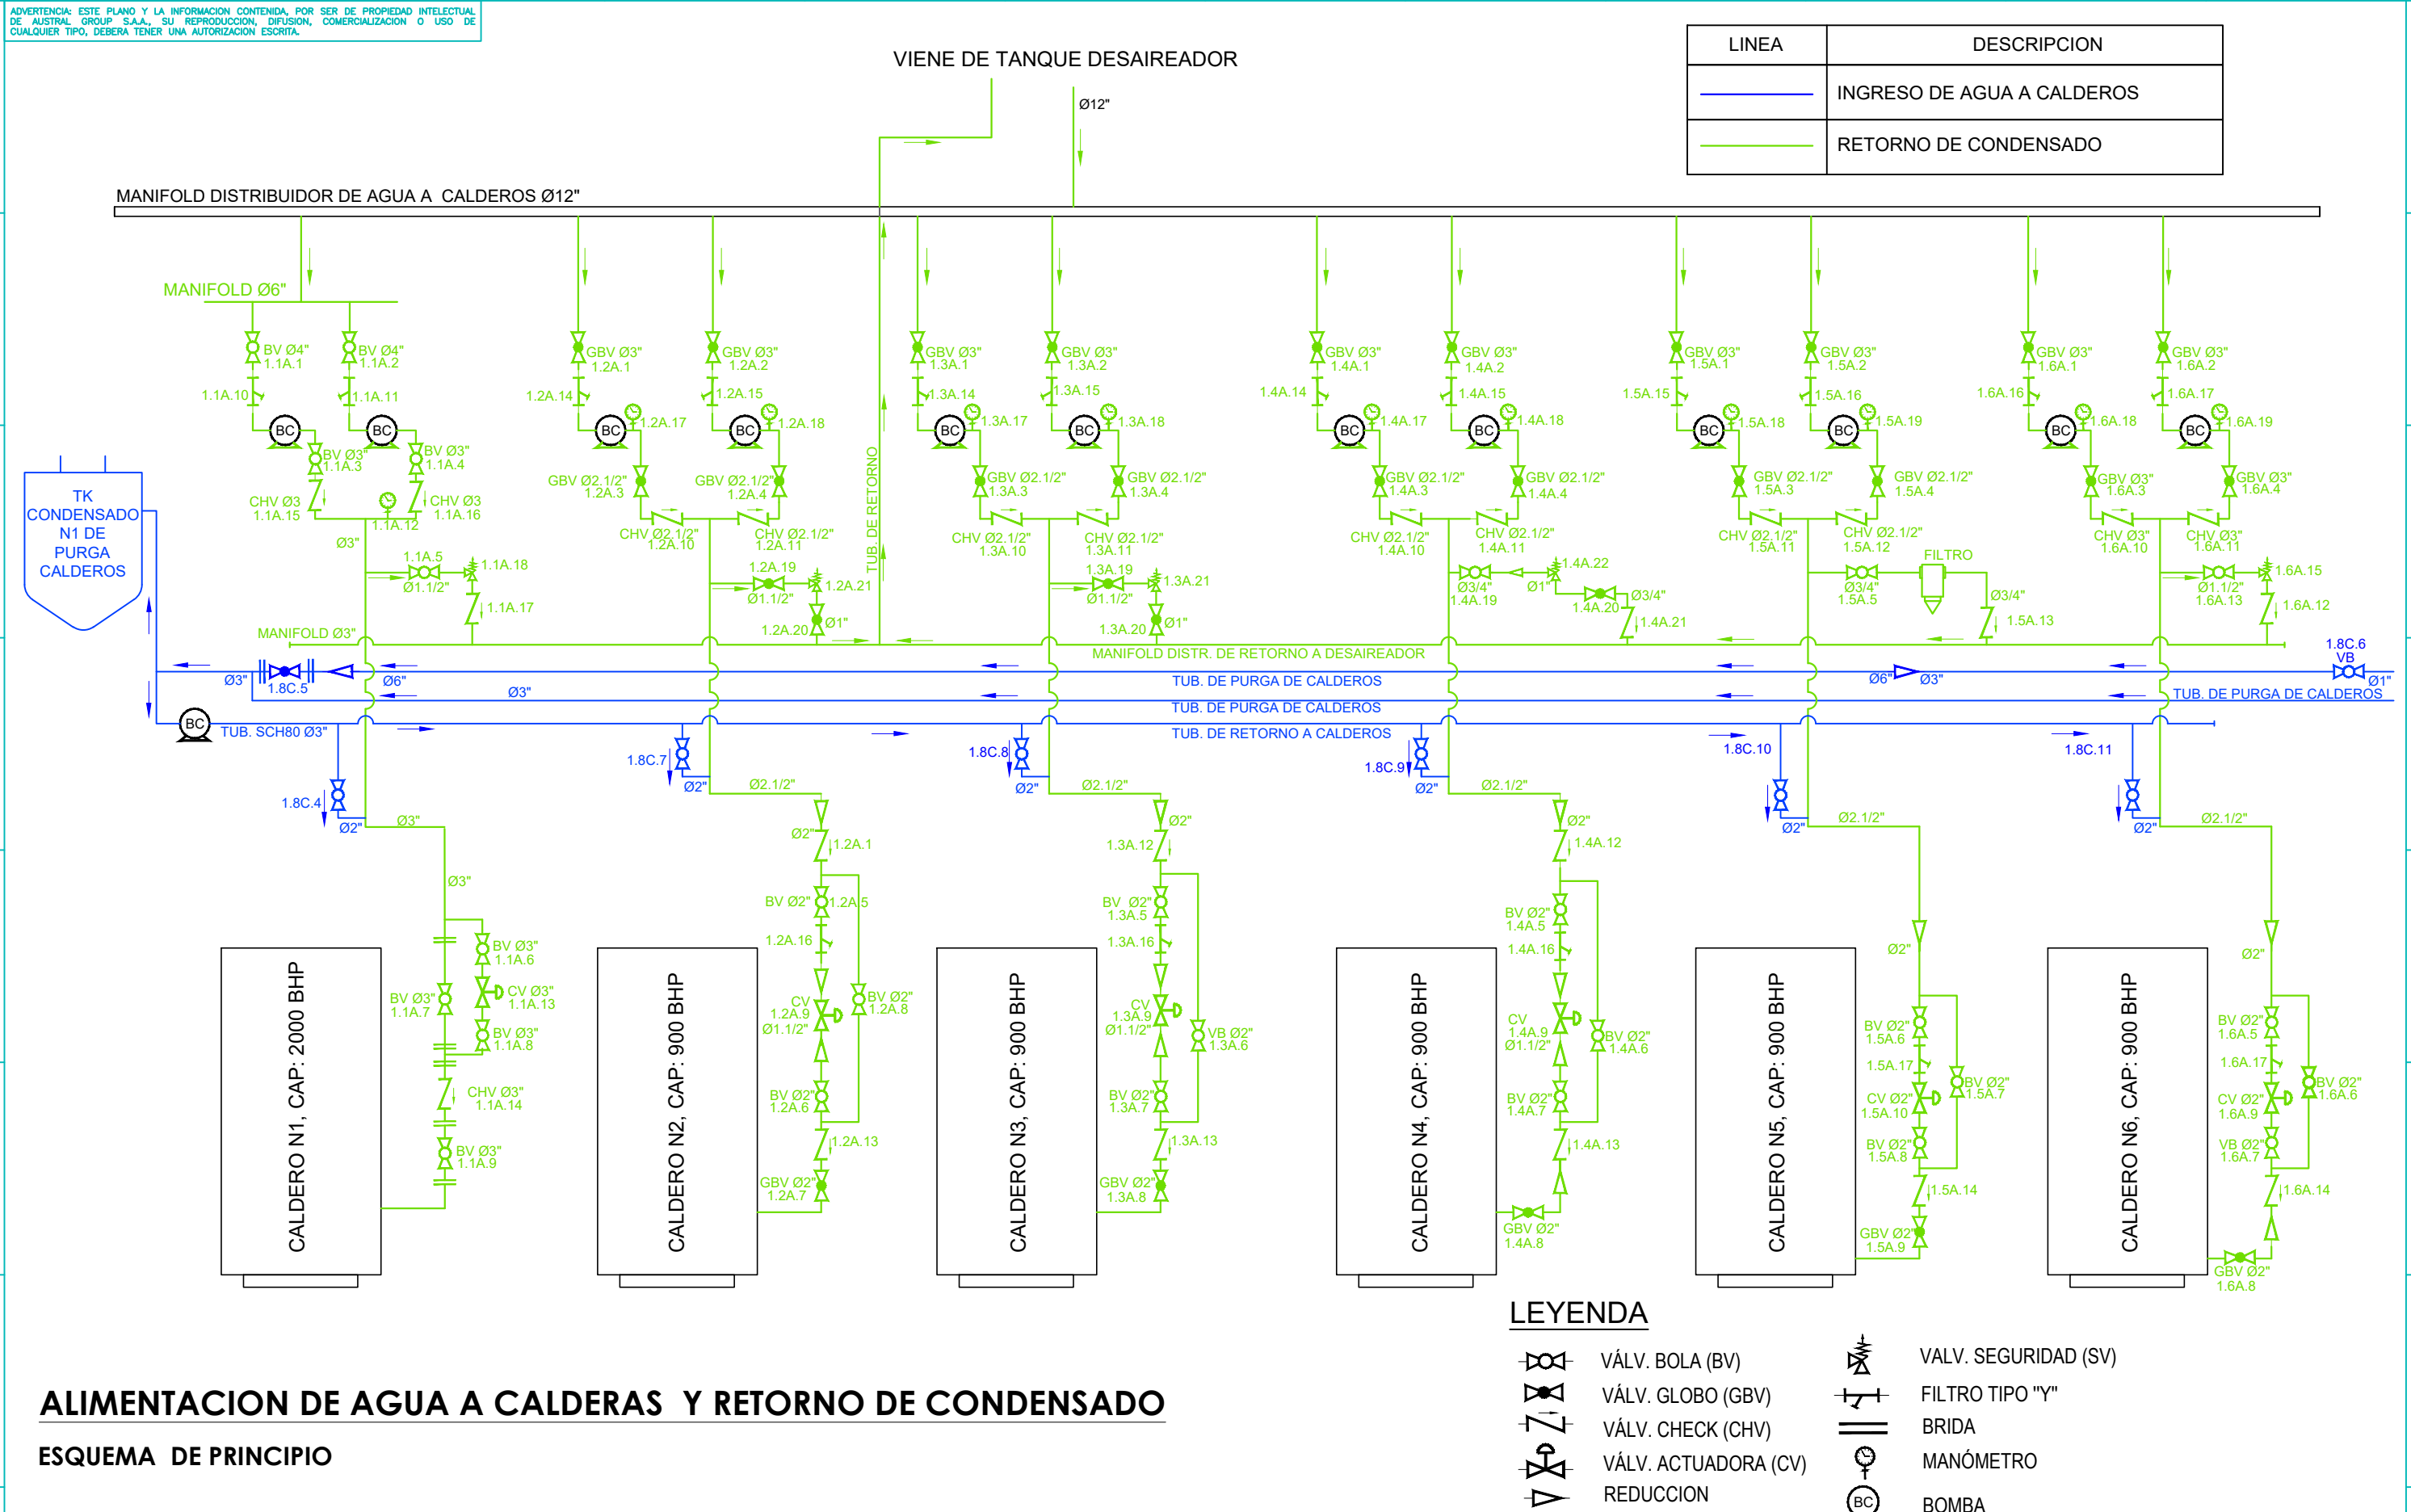

						Austral Group S.A.A. Austevoll Seated Company	CLIENTE: AUSTRAL GROUP S.A.A. PLANTA COISHCO			
							TITULO: ZONA DE CALDERAS ESQUEMA DE PRINCIPIO ALIMENTACION DE AGUA A CALDERAS			
				J.A.M	—		FORMATO	ESC.	PLANO N.º	PAG:
	REV.	FECHA	DESCRIPCION DE REVISION	REVISADO	APROBADO		A3	IND.	AU-COI-VAPOR-P09	1/2
							DISEÑADO POR: — FECHA: JUNIO 2024			
							DIBUJADO POR: O.C.R. FECHA: JUNIO 2024			
							REVISADO POR: J.A.M FECHA: JUNIO 2024			
							APROBADO POR: — FECHA: JUNIO 2024			