
ADVERTENCIA: ESTE PLANO Y LA INFORMACION CONTENIDA, POR SER DE PROPIEDAD INTELECTUAL DE AUSTRAL GROUP S.A.A., SU REPRODUCCION, DIFUSION, COMERCIALIZACION O USO DE CUALQUIER TIPO, DEBERA TENER UNA AUTORIZACION ESCRITA.

LINEA	DESCRIPCION
	INGRESO DE AGUA A CALDEROS
	RETORNO DE CONDENSADO

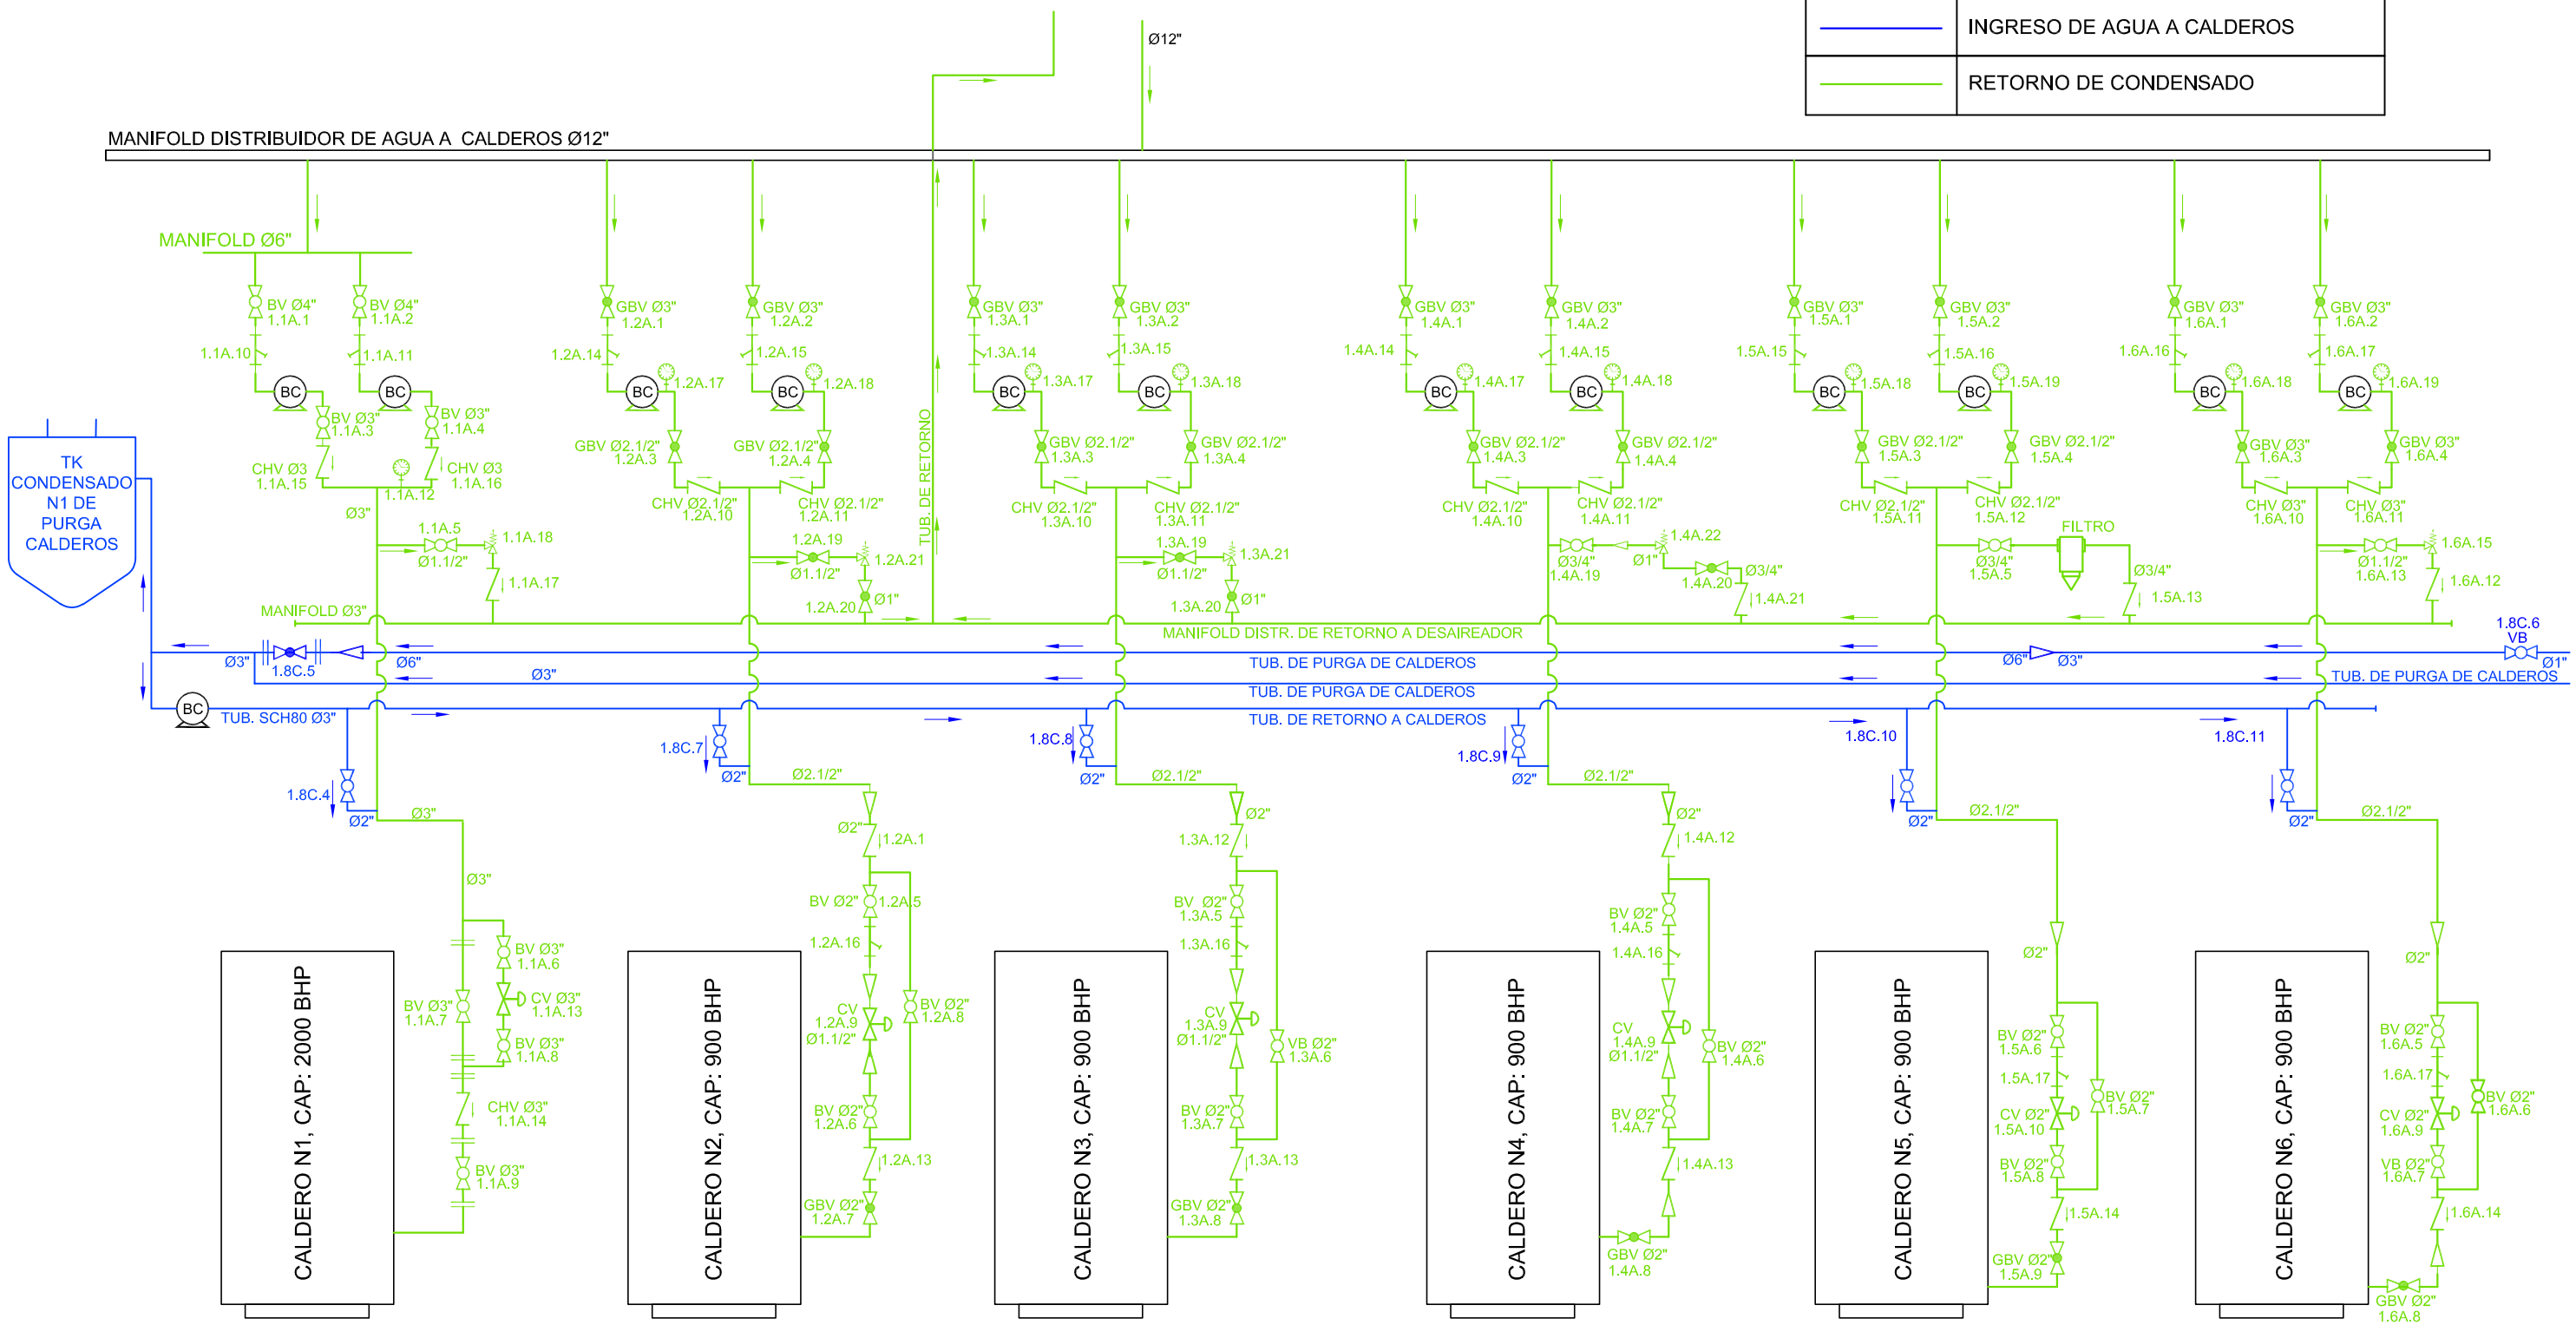

LEYENDA

- VÁLV. BOLA (BV)
- VÁLV. GLOBO (GBV)
- VÁLV. CHECK (CHV)
- VÁLV. ACTUADORA (CV)
- REDUCCION
- VALV. SEGURIDAD (SV)
- FILTRO TIPO "Y"
- BRIDA
- MANÓMETRO
- BOMBA

ALIMENTACION DE AGUA A CALDERAS Y RETORNO DE CONDENSADO

ESQUEMA DE PRINCIPIO

REV.	FECHA	DESCRIPCION DE REVISION		
			O.C.R.	J.A.M
			REVISADO	APROBADO

DISEÑADO POR:	–	FECHA:	JUNIO 2024
DIBUJADO POR:	O.C.R.	FECHA:	JUNIO 2024
REVISADO POR:	O.C.R.	FECHA:	JUNIO 2024
APROBADO POR:	J.A.M.	FECHA:	JUNIO 2024

Austral Group S.A.A.
Austevoll Seafood Company

CLIENTE: AUSTRAL GROUP S.A.A.
PLANTA COISHCO

TITULO: ZONA DE CALDERAS
ESQUEMA DE PRINCIPIO
ALIMENTACION DE AGUA A CALDERAS

FORMATO	ESC.	PLANO N.°	REV:
A3	IND.	AU–COI–VAPOR–P09	A