


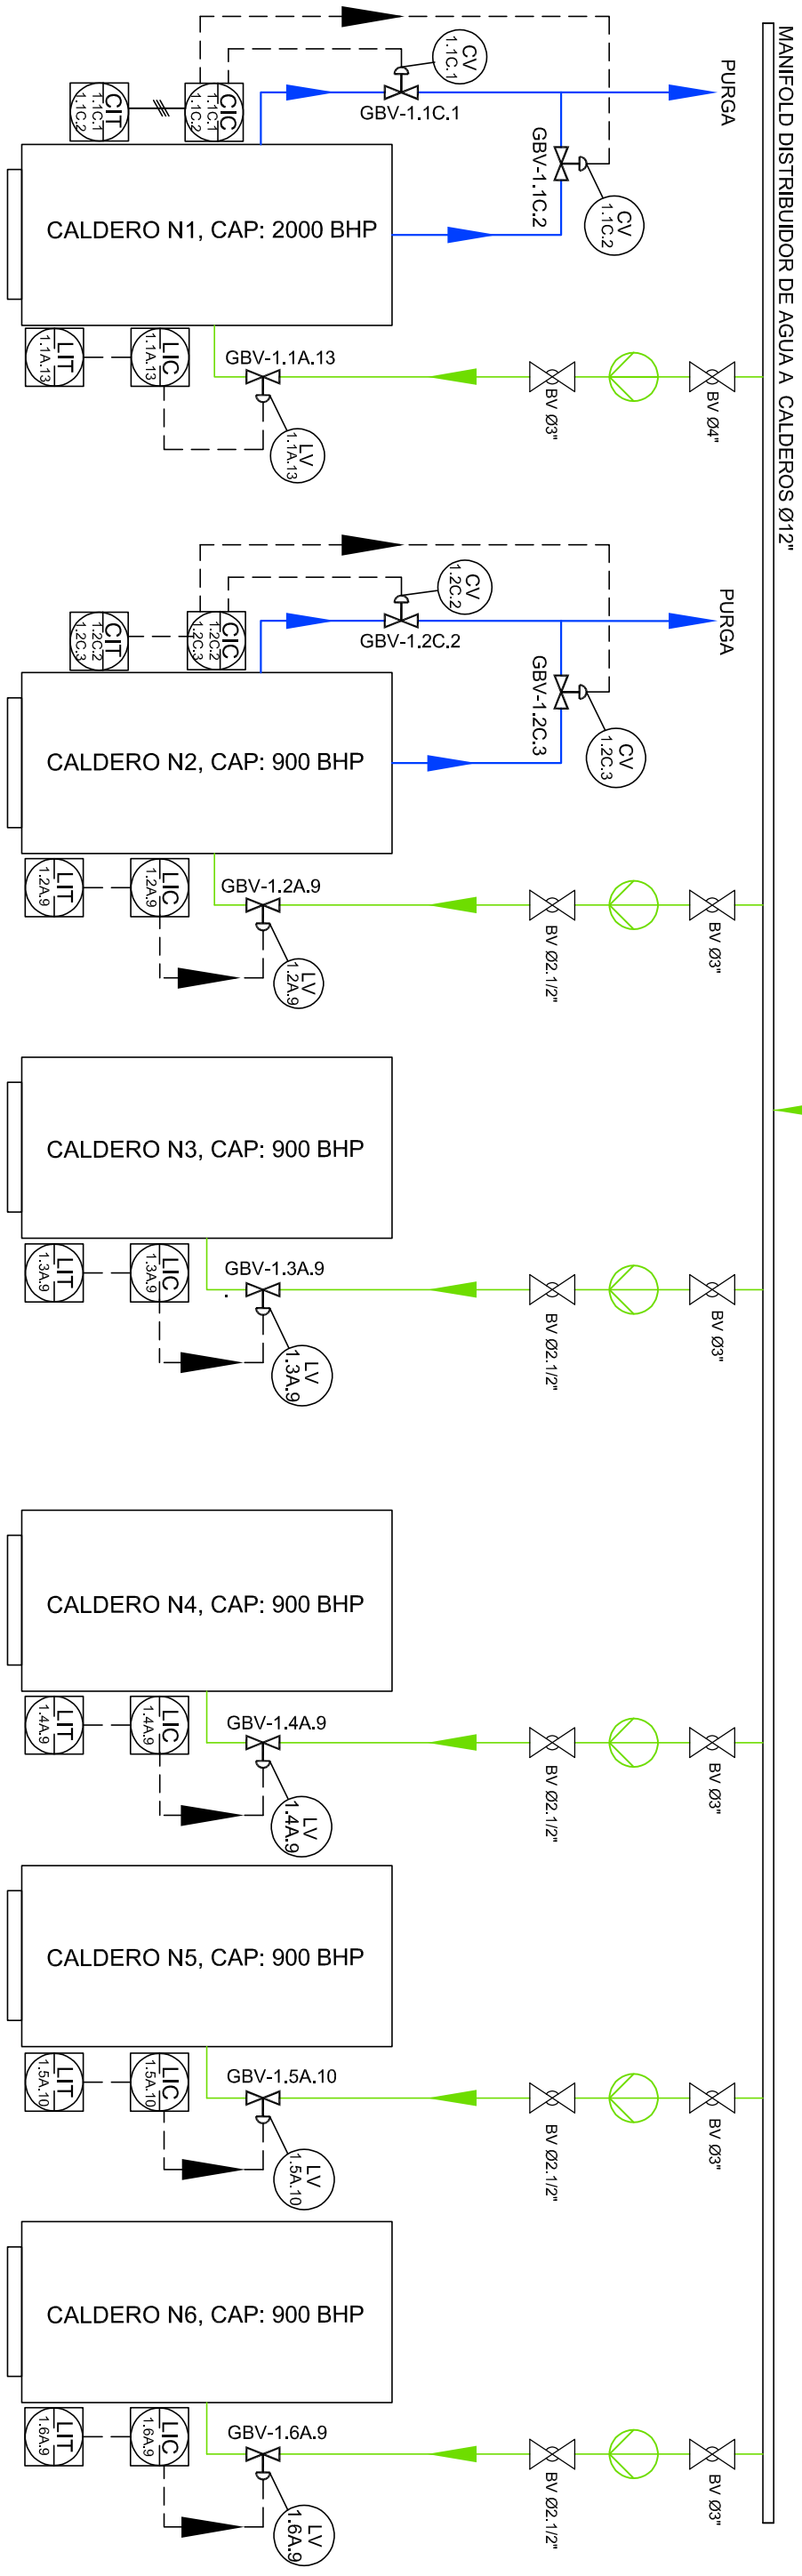

VIENE DE TANQUE DESAIREADOR

ITEM	LINEA	DESCRIPCIÓN
2	CONDENSADO	
3	AGUA BLANDA	
4	ELECTRICO	
5	HIDRAULICO	
6	MECANICO	

ALIMENTACION DE AGUA A CALDERAS Y PURGA DE CONDENSADO

ESQUEMA P&DI

[illegible]