


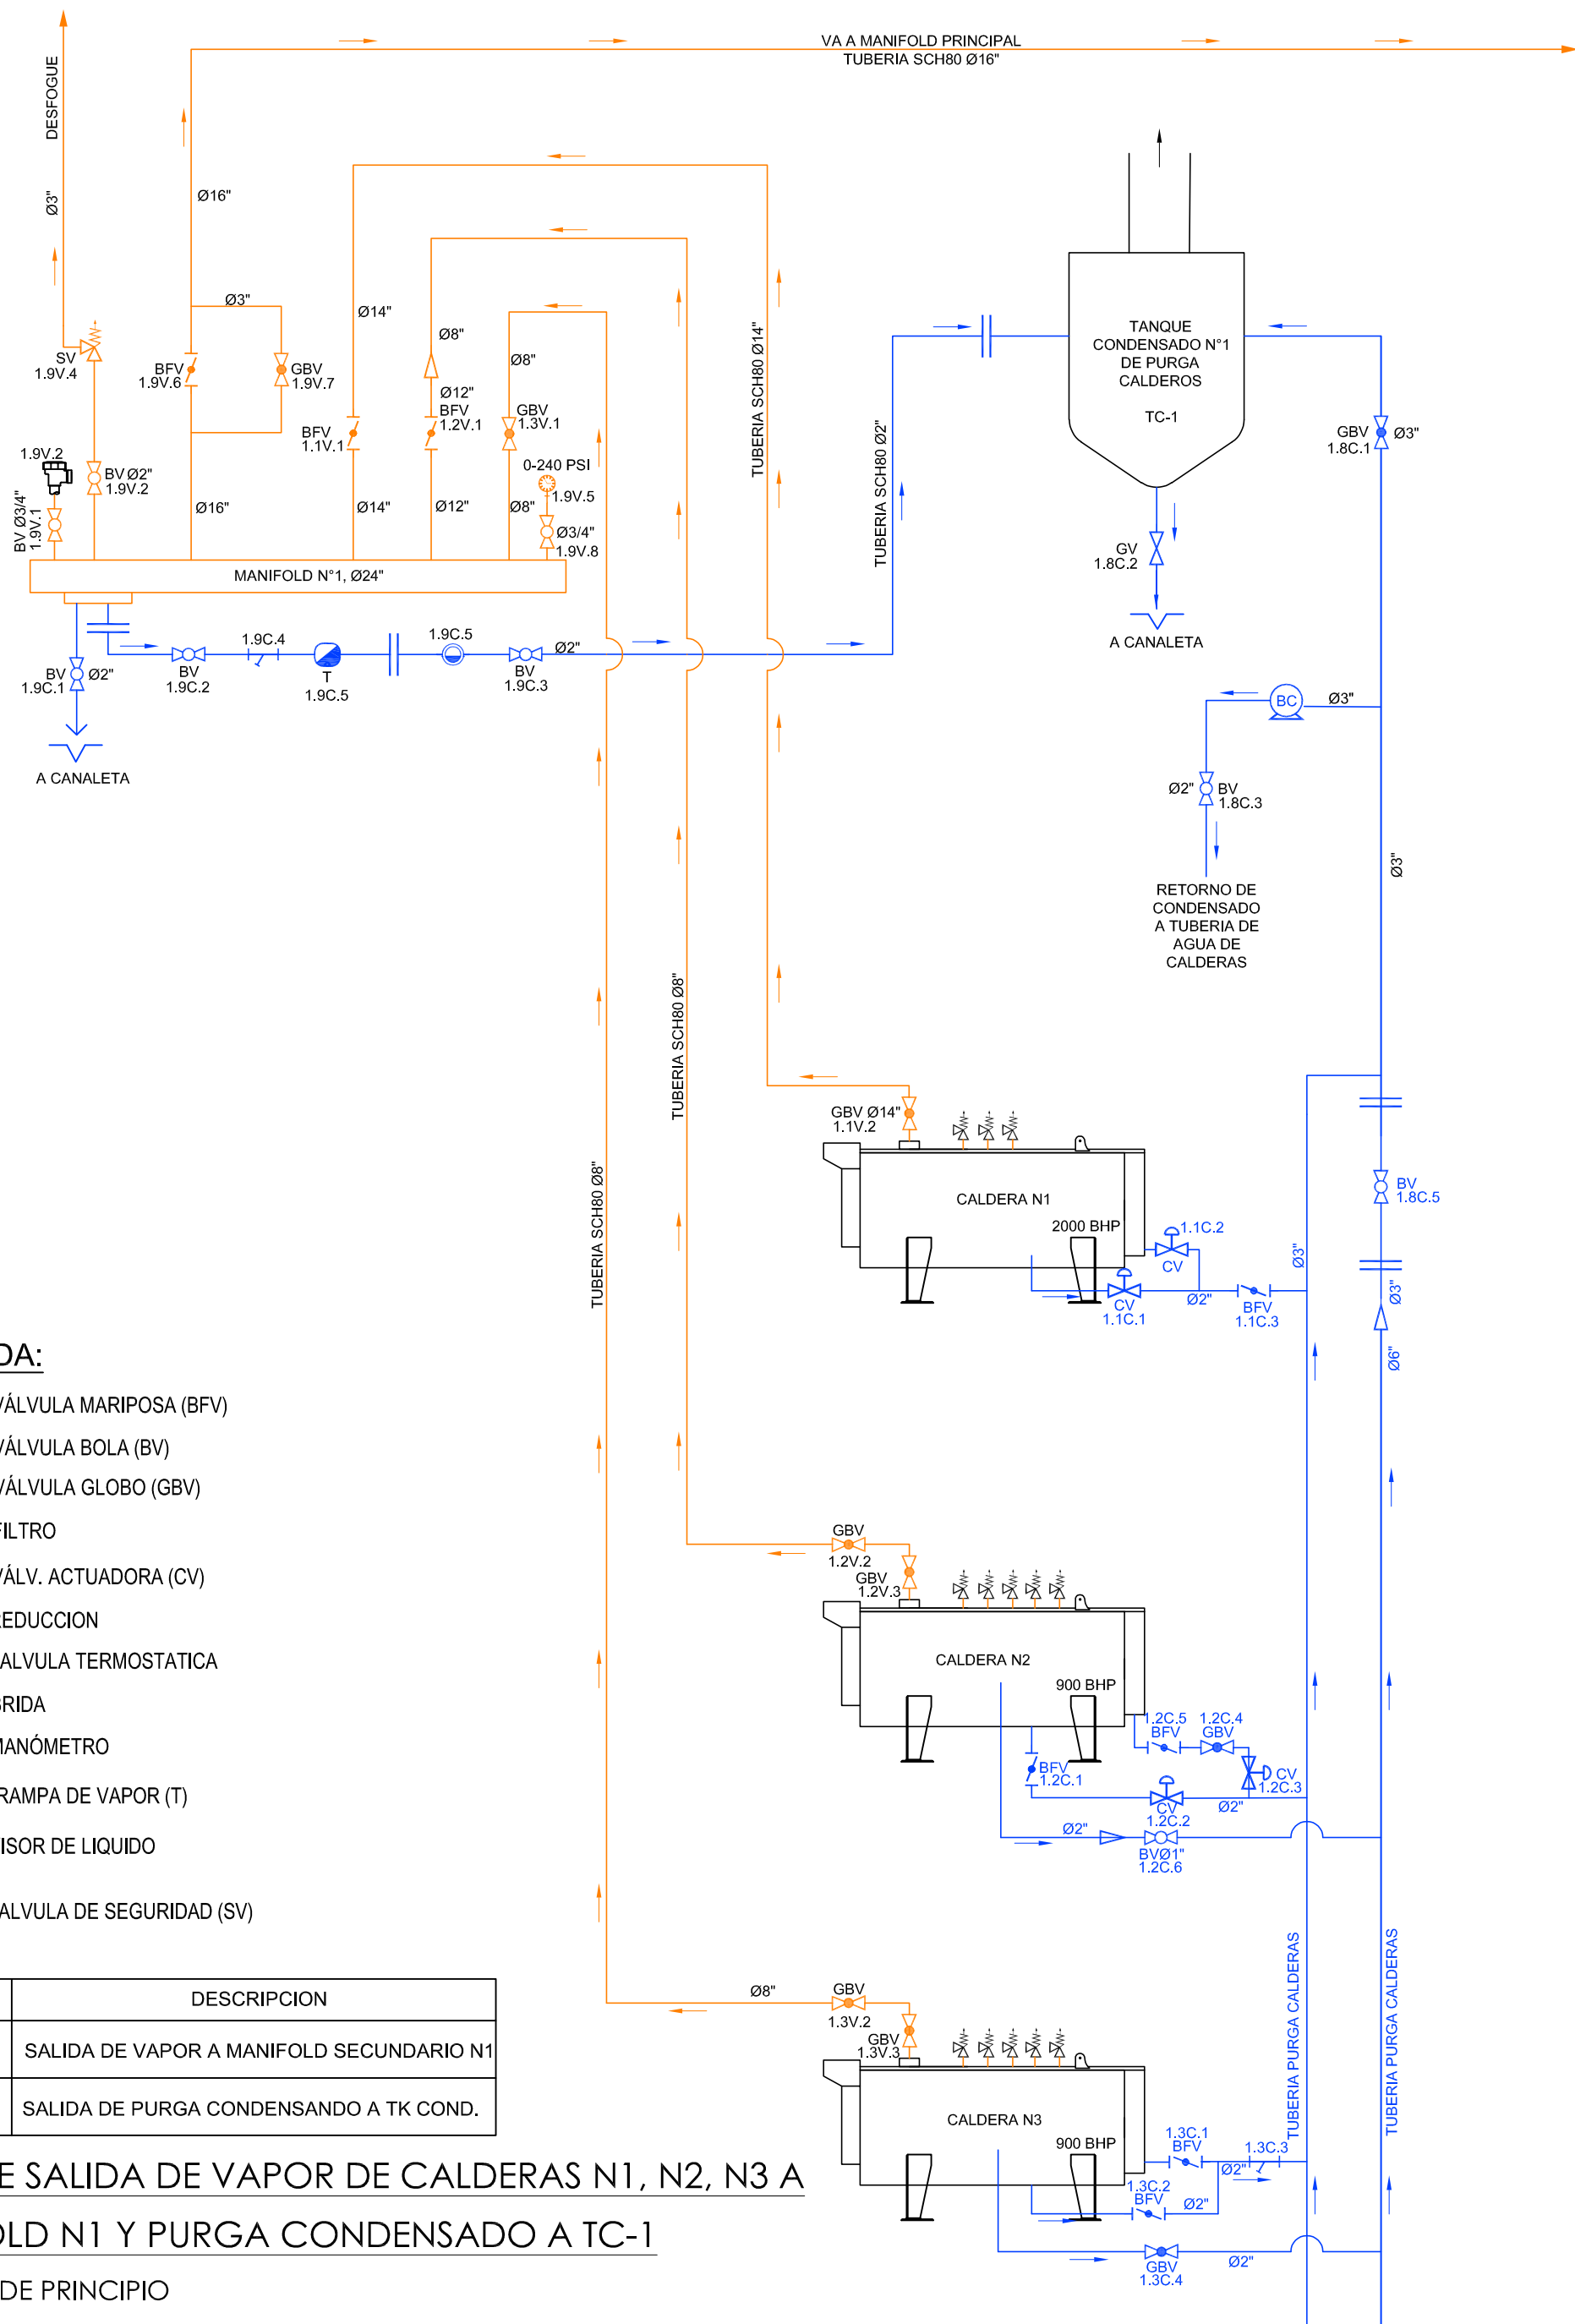

LEYENDA:

- | | |
|---|---------------------------|
|  | VÁLVULA MARIPOSA (BFV) |
|  | VÁLVULA BOLA (BV) |
|  | VÁLVULA GLOBO (GBV) |
|  | FILTRO |
|  | VÁLV. ACTUADORA (CV) |
|  | REDUCCION |
|  | VALVULA TERMOSTATICA |
|  | BRIDA |
|  | MANÓMETRO |
|  | TRAMPA DE VAPOR (T) |
|  | VISOR DE LIQUIDO |
|  | VALVULA DE SEGURIDAD (SV) |

LINEA	DESCRIPCION
	SALIDA DE VAPOR A MANIFOLD SECUNDARIO N1
	SALIDA DE PURGA CONDENSANDO A TK COND.

LINEA DE SALIDA DE VAPOR DE CALDERAS N1, N2, N3 A
MANIFOLD N1 Y PURGA CONDENSADO A TC-1
ESQUEMA DE PRINCIPIO

				 Austral Group S.A.A. Austevoll Seafood Company	CLIENTE: AUSTRAL GROUP S.A.A. PLANTA COISHCO						
					TITULO: ZONA DECALDERAS ESQUEMA DE PRINCIPIO LINEA SALIDA VAPOR DE CALDERAS N1, N2, N3 A MANIFOLD N1 Y PURGA DE CONDENSADO A TC-1						
			DISEÑADO POR:		FECHA:	JUNIO 2024	FORMATO	ESC.	PLANO N.º	PAG:	
			DIBUJADO POR:		OC.R.	FECHA:	JUNIO 2024	A3	S/E	AU-COI-VAPOR-P12	1/2
			REVISADO POR:		J.A.M.	FECHA:	JUNIO 2024				
			APROBADO POR:			FECHA:	JUNIO 2024				
DESCRIPCION DE REVISION	REVISADO	APROBADO	J.A.M								