


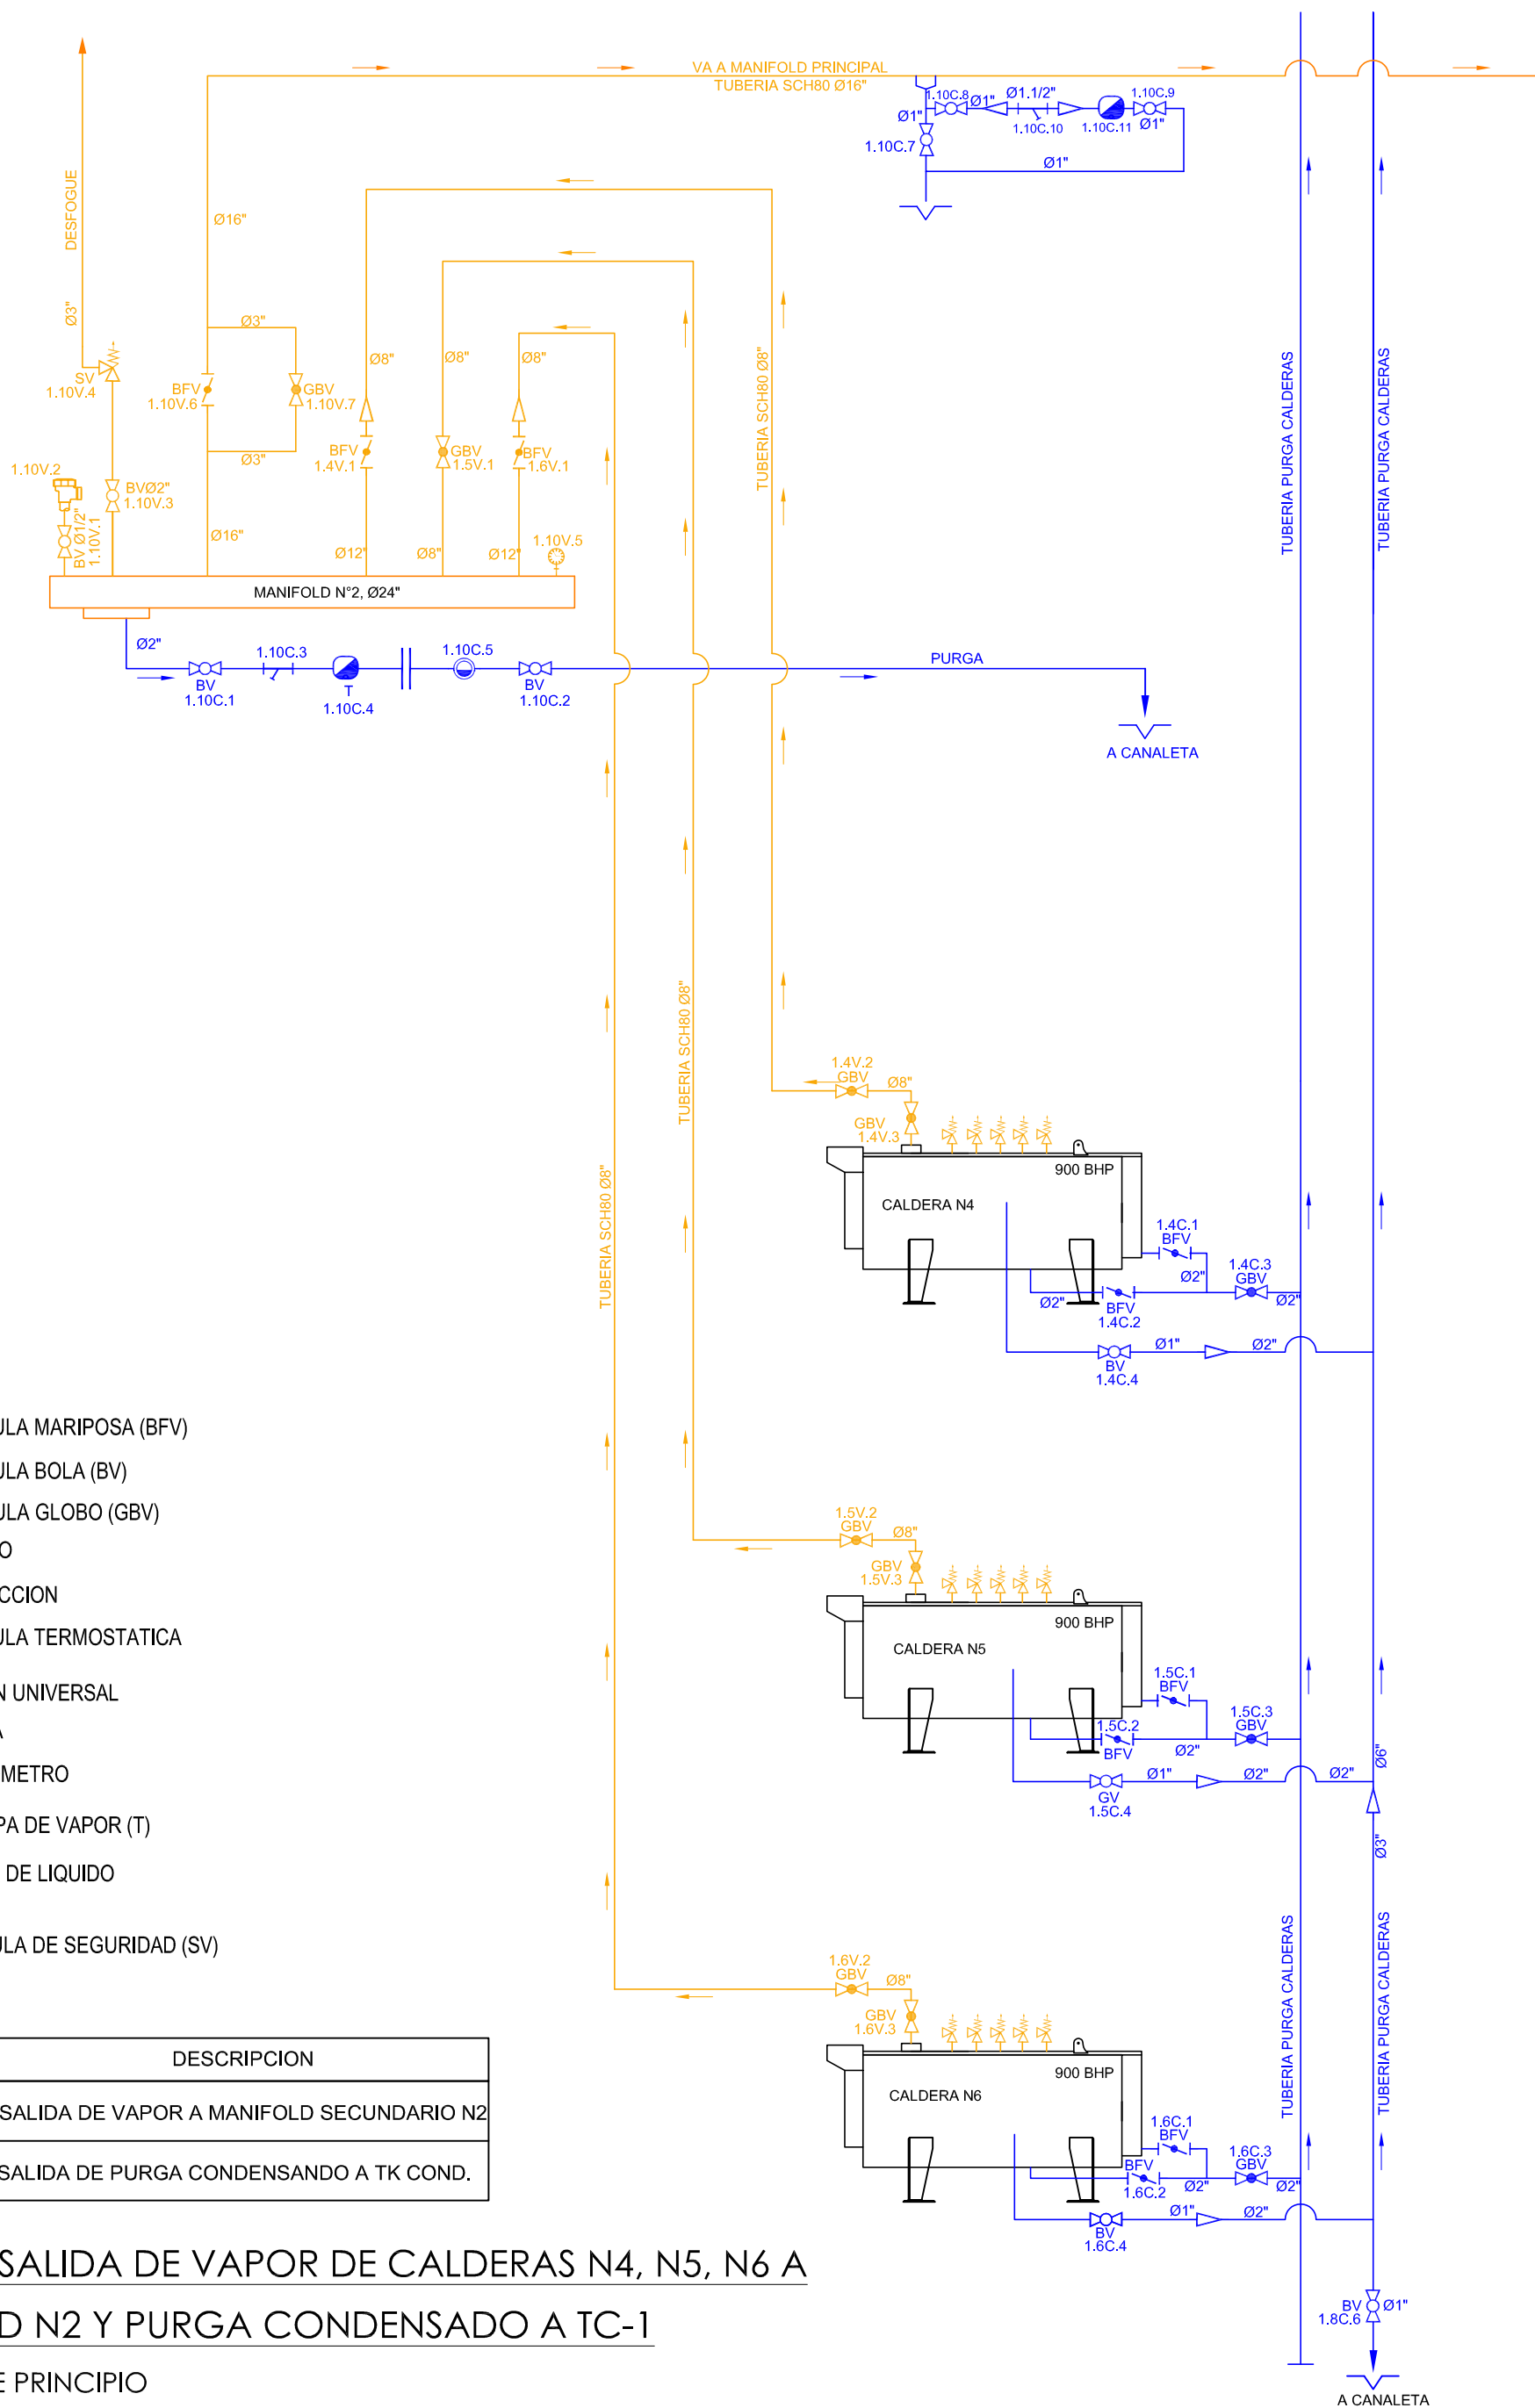

LEYENDA:

- | | |
|---|---------------------------|
|  | VÁLVULA MARIPOSA (BFV) |
|  | VÁLVULA BOLA (BV) |
|  | VÁLVULA GLOBO (GBV) |
|  | FILTRO |
|  | REDUCCION |
|  | VALVULA TERMOSTATICA |
|  | UNION UNIVERSAL |
|  | BRIDA |
|  | MANÓMETRO |
|  | TRAMPA DE VAPOR (T) |
|  | VISOR DE LIQUIDO |
|  | VALVULA DE SEGURIDAD (SV) |

LINEA	DESCRIPCION
	SALIDA DE VAPOR A MANIFOLD SECUNDARIO N2
	SALIDA DE PURGA CONDENSANDO A TK COND.

LINEA DE SALIDA DE VAPOR DE CALDERAS N4, N5, N6 A
MANIFOLD N2 Y PURGA CONDENSADO A TC-1

ESQUEMA DE PRINCIPIO

				 Austral Group S.A.A. Austevoll Seafood Company	CLIENTE: AUSTRAL GROUP S.A.A. PLANTA COISHCO			
					TITULO: ZONA DE CALDEROS ESQUEMA DE PRINCIPIO LINEA SALIDA VAPOR DE CALDERAS N4, N5, N6 A MANIFOLD N2 Y PURGA DE CONDENSADO A TC-1			
			DISEÑADO POR: FECHA: JUNIO 2024		FORMATO	ESC.	PLANO N.º	PAG:
	J.A.M		DIBUJADO POR: O.C.R. FECHA: JUNIO 2024		A3	S/E	AU-COI-VAPOR-P14	1/2
DESCRIPCION DE REVISION	REVISADO	APROBADO	REVISADO POR: J.A.M. FECHA: JUNIO 2024 APROBADO POR: FECHA: JUNIO 2024					