


LINEAS DE SALIDA DE VAPOR DE CALDERAS N°4, N°5 Y N°6 A MANIFOLD N°2

ISOMÉTRICO - LINEA DE VAPOR Y SALIDA PURGA CONDENSADO

LEYENDA	
ITEM	DESCRIPCIÓN
1	LINEA DE VAPOR VIVO - 7.5 BAR
2	LINEA DE CONDENSADO - 6 BAR

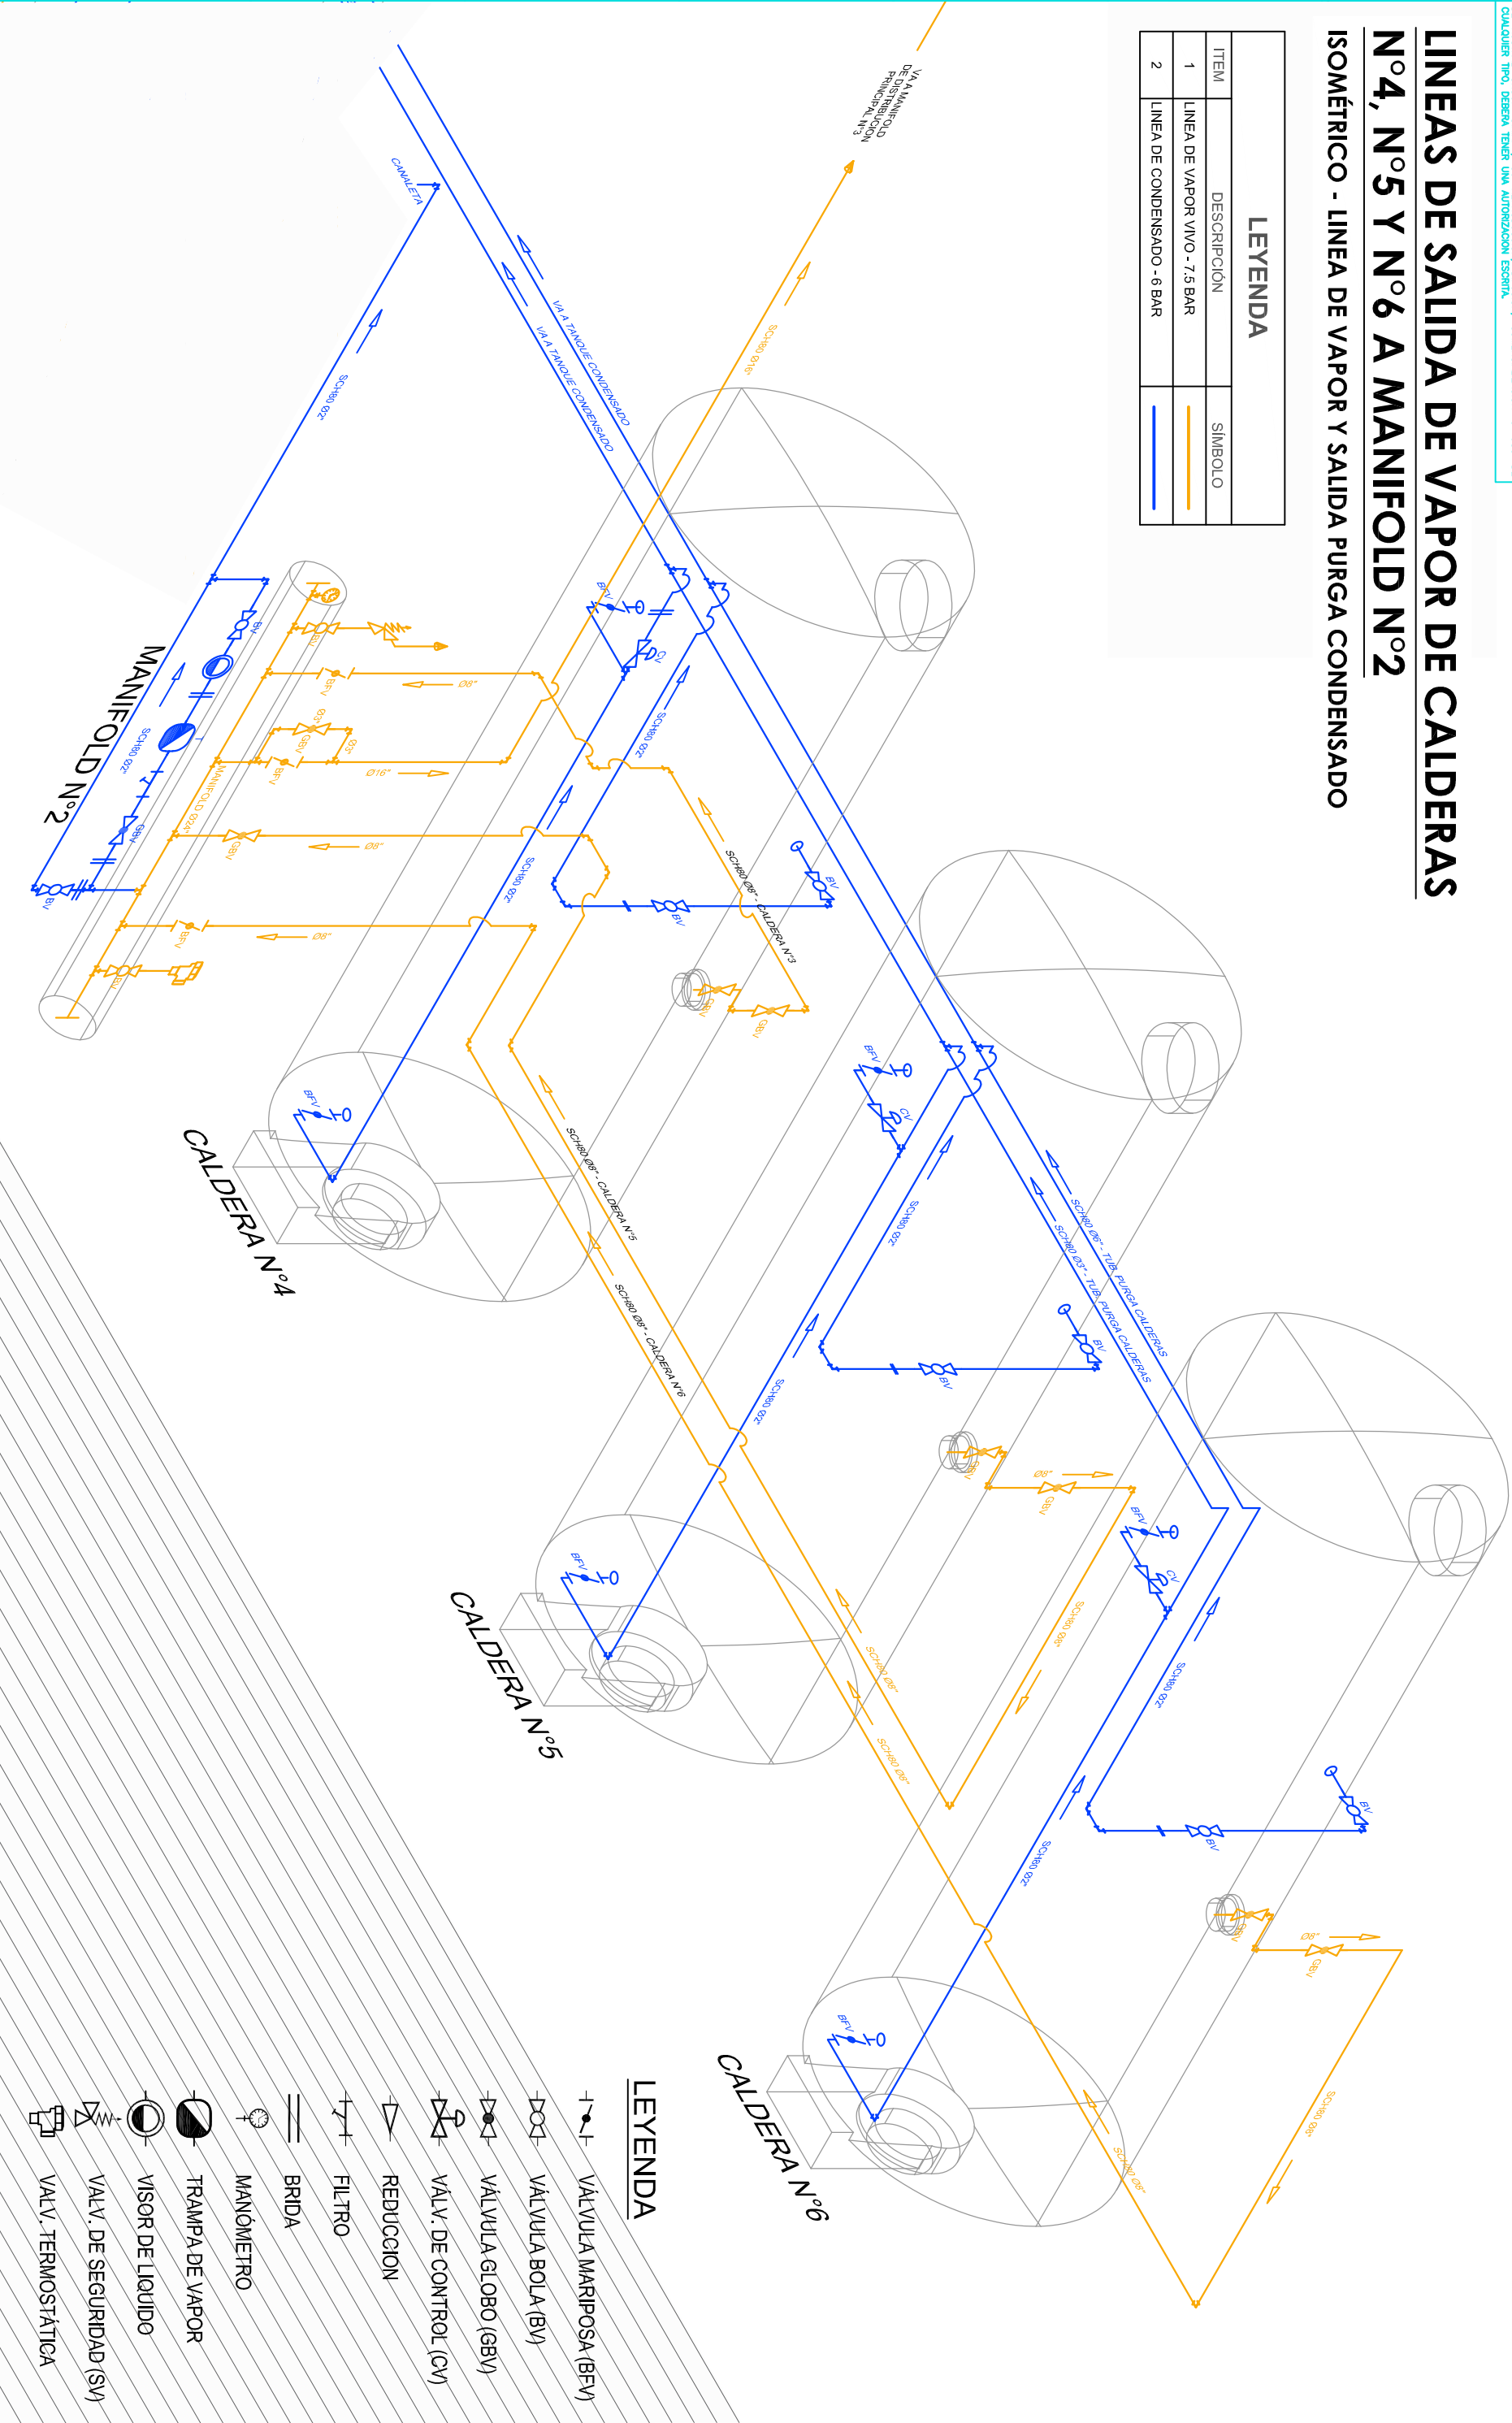

LEYENDA	
+	VÁLVULA MARIPOSA (BV)
+	VÁLVULA BOLA (BV)
+	VÁLVULA GLOBO (GBV)
+	VÁLV. DE CONTROL (CV)
+	REDUCCION
+	FILTRO
+	BRIDA
+	MANÓMETRO
+	TRAMPA DE VAPOR
+	VISOR DE LIQUIDO
+	VALV. DE SEGURIDAD (SV)
+	VALV. TERMOSTÁTICA

CLIENTE:	
AUSTRAL GROUP S.A.A. PLANTA COISHCO	
TÍTULO:	
AUSTRAL – PLANTA DE HARINA PLANO ISOMÉTRICO – REDES DE VAPOR Y PURGA CONDENSADO LINEAS DE SALIDA DE VAPOR DE CALDERAS N°4, N°5 Y N°6 A MANIFOLD N°2	
FORMATO	
A3	S/C
REV.	
1	A

--	--	

DISEÑADO POR:	
J.G.R.	FECHA: JUNIO 2024
REVISADO POR:	
J.A.M.	FECHA: JUNIO 2024
APROBADO POR:	
FECHA: JUNIO 2024	



CLIENTE:	
AUSTRAL GROUP S.A.A. PLANTA COISHCO	
TÍTULO:	
AUSTRAL – PLANTA DE HARINA PLANO ISOMÉTRICO – REDES DE VAPOR Y PURGA CONDENSADO LINEAS DE SALIDA DE VAPOR DE CALDERAS N°4, N°5 Y N°6 A MANIFOLD N°2	
FORMATO	
A3	S/C
REV.	
1	A