ADVERTENCIA: ESTE PLANO Y LA INFORMACION CONTENIDA, POR SER DE PROPIEDAD INTELECTUAL DE AUSTRAL GROUP S.A.A., SU REPRODUCCION, DIFUSION, COMERCIALIZACION O USO DE CUALQUIER TIPO, DEBERA TENER UNA AUTORIZACION ESCRITA.

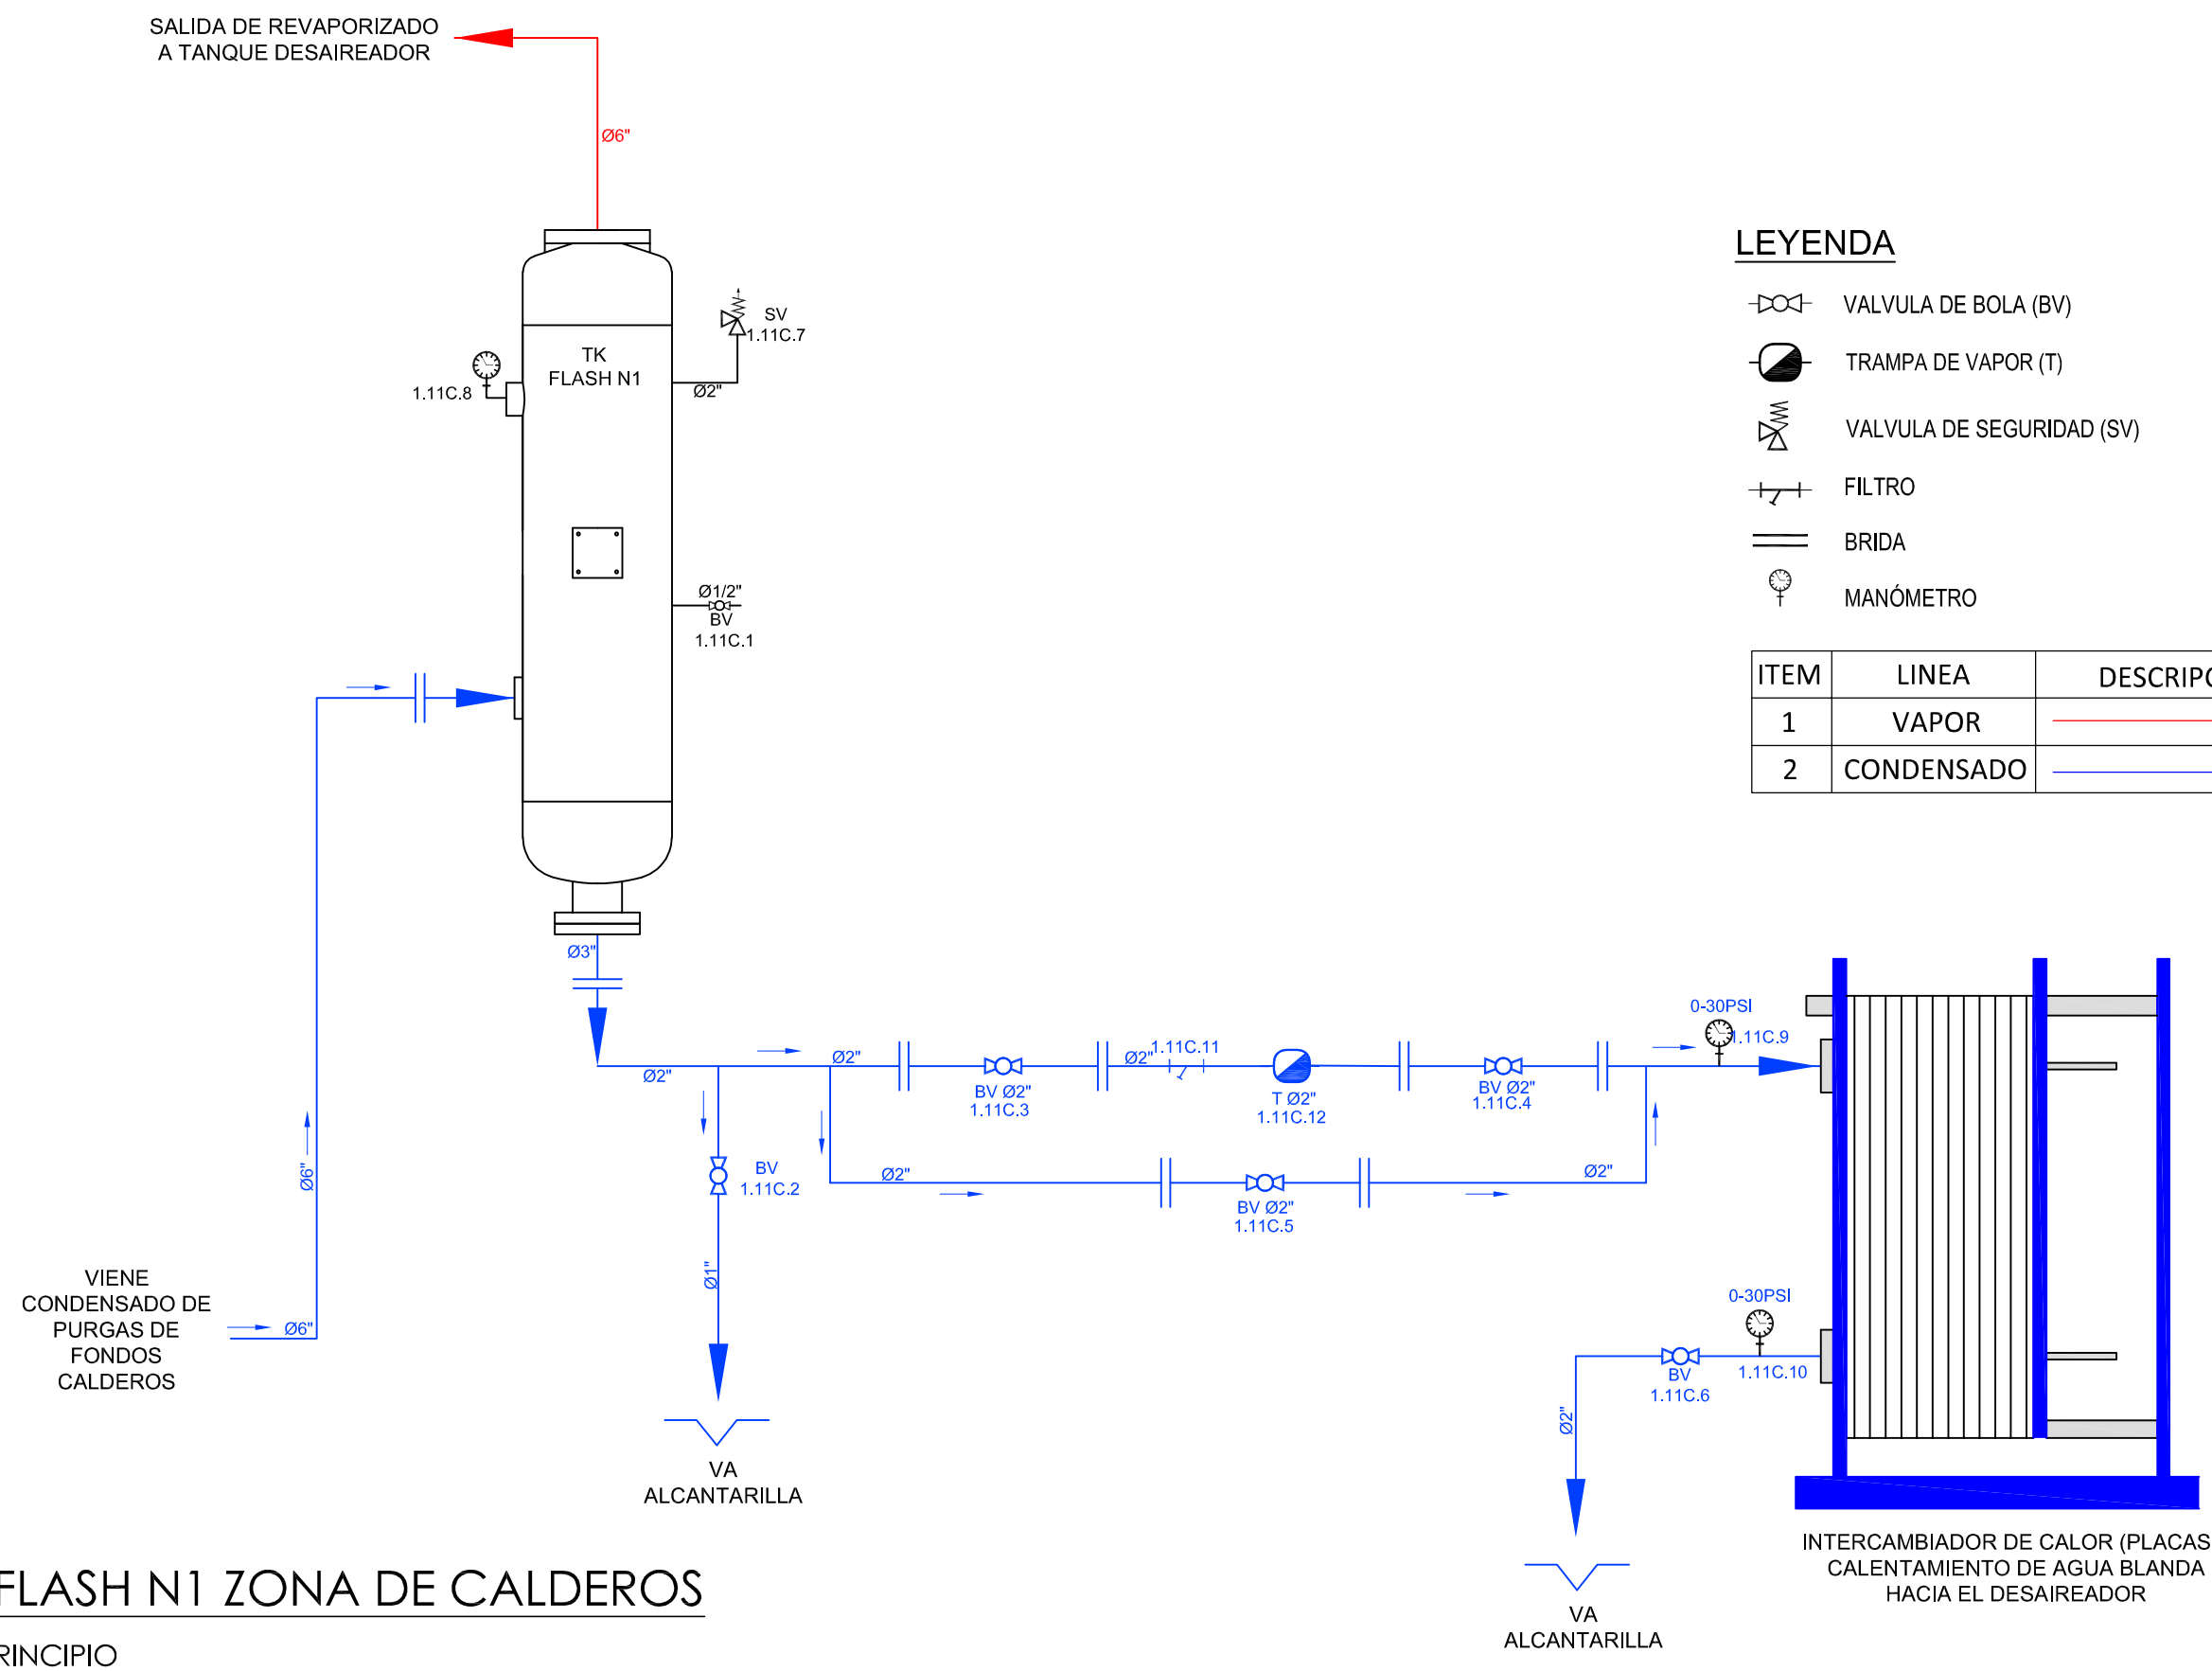

LEYENDA

- VALVULA DE BOLA (BV)
- TRAMPA DE VAPOR (T)
- VALVULA DE SEGURIDAD (SV)
- FILTRO
- BRIDA
- MANÓMETRO

ITEM	LINEA	DESCRIPCIÓN
1	VAPOR	
2	CONDENSADO	

TANQUE FLASH N1 ZONA DE CALDEROS

ESQUEMA DE PRINCIPIO

REV.	FECHA	DESCRIPCION DE REVISION	APROBADO
			J.A.M

DISEÑADO POR:		FECHA:	JUNIO 2024
DIBUJADO POR:	O.C.R.	FECHA:	JUNIO 2024
REVISADO POR:	O.C.R.	FECHA:	JUNIO 2024
APROBADO POR:	J.A.M.	FECHA:	JUNIO 2024

Austral Group S.A.A.
Austevoll Seafood Company

CLIENTE: AUSTRAL GROUP S.A.A.
PLANTA COISHCO

TITULO: ZONA DE CALDEROS
ESQUEMA DE PRINCIPIOS
TANQUE FLASH N1 – ZONA DE CALDEROS

FORMATO	ESC.	PLANO N.°	PAG:
A3	S/E	AU–COI–VAPOR–P17	1/2