


MANIFOLD DISTRIBUIDOR PRINCIPAL N°3 A PLANTA DE HARINA

ISOMETRÍCO - LINEAS DE VAPOR Y CONDENSADO

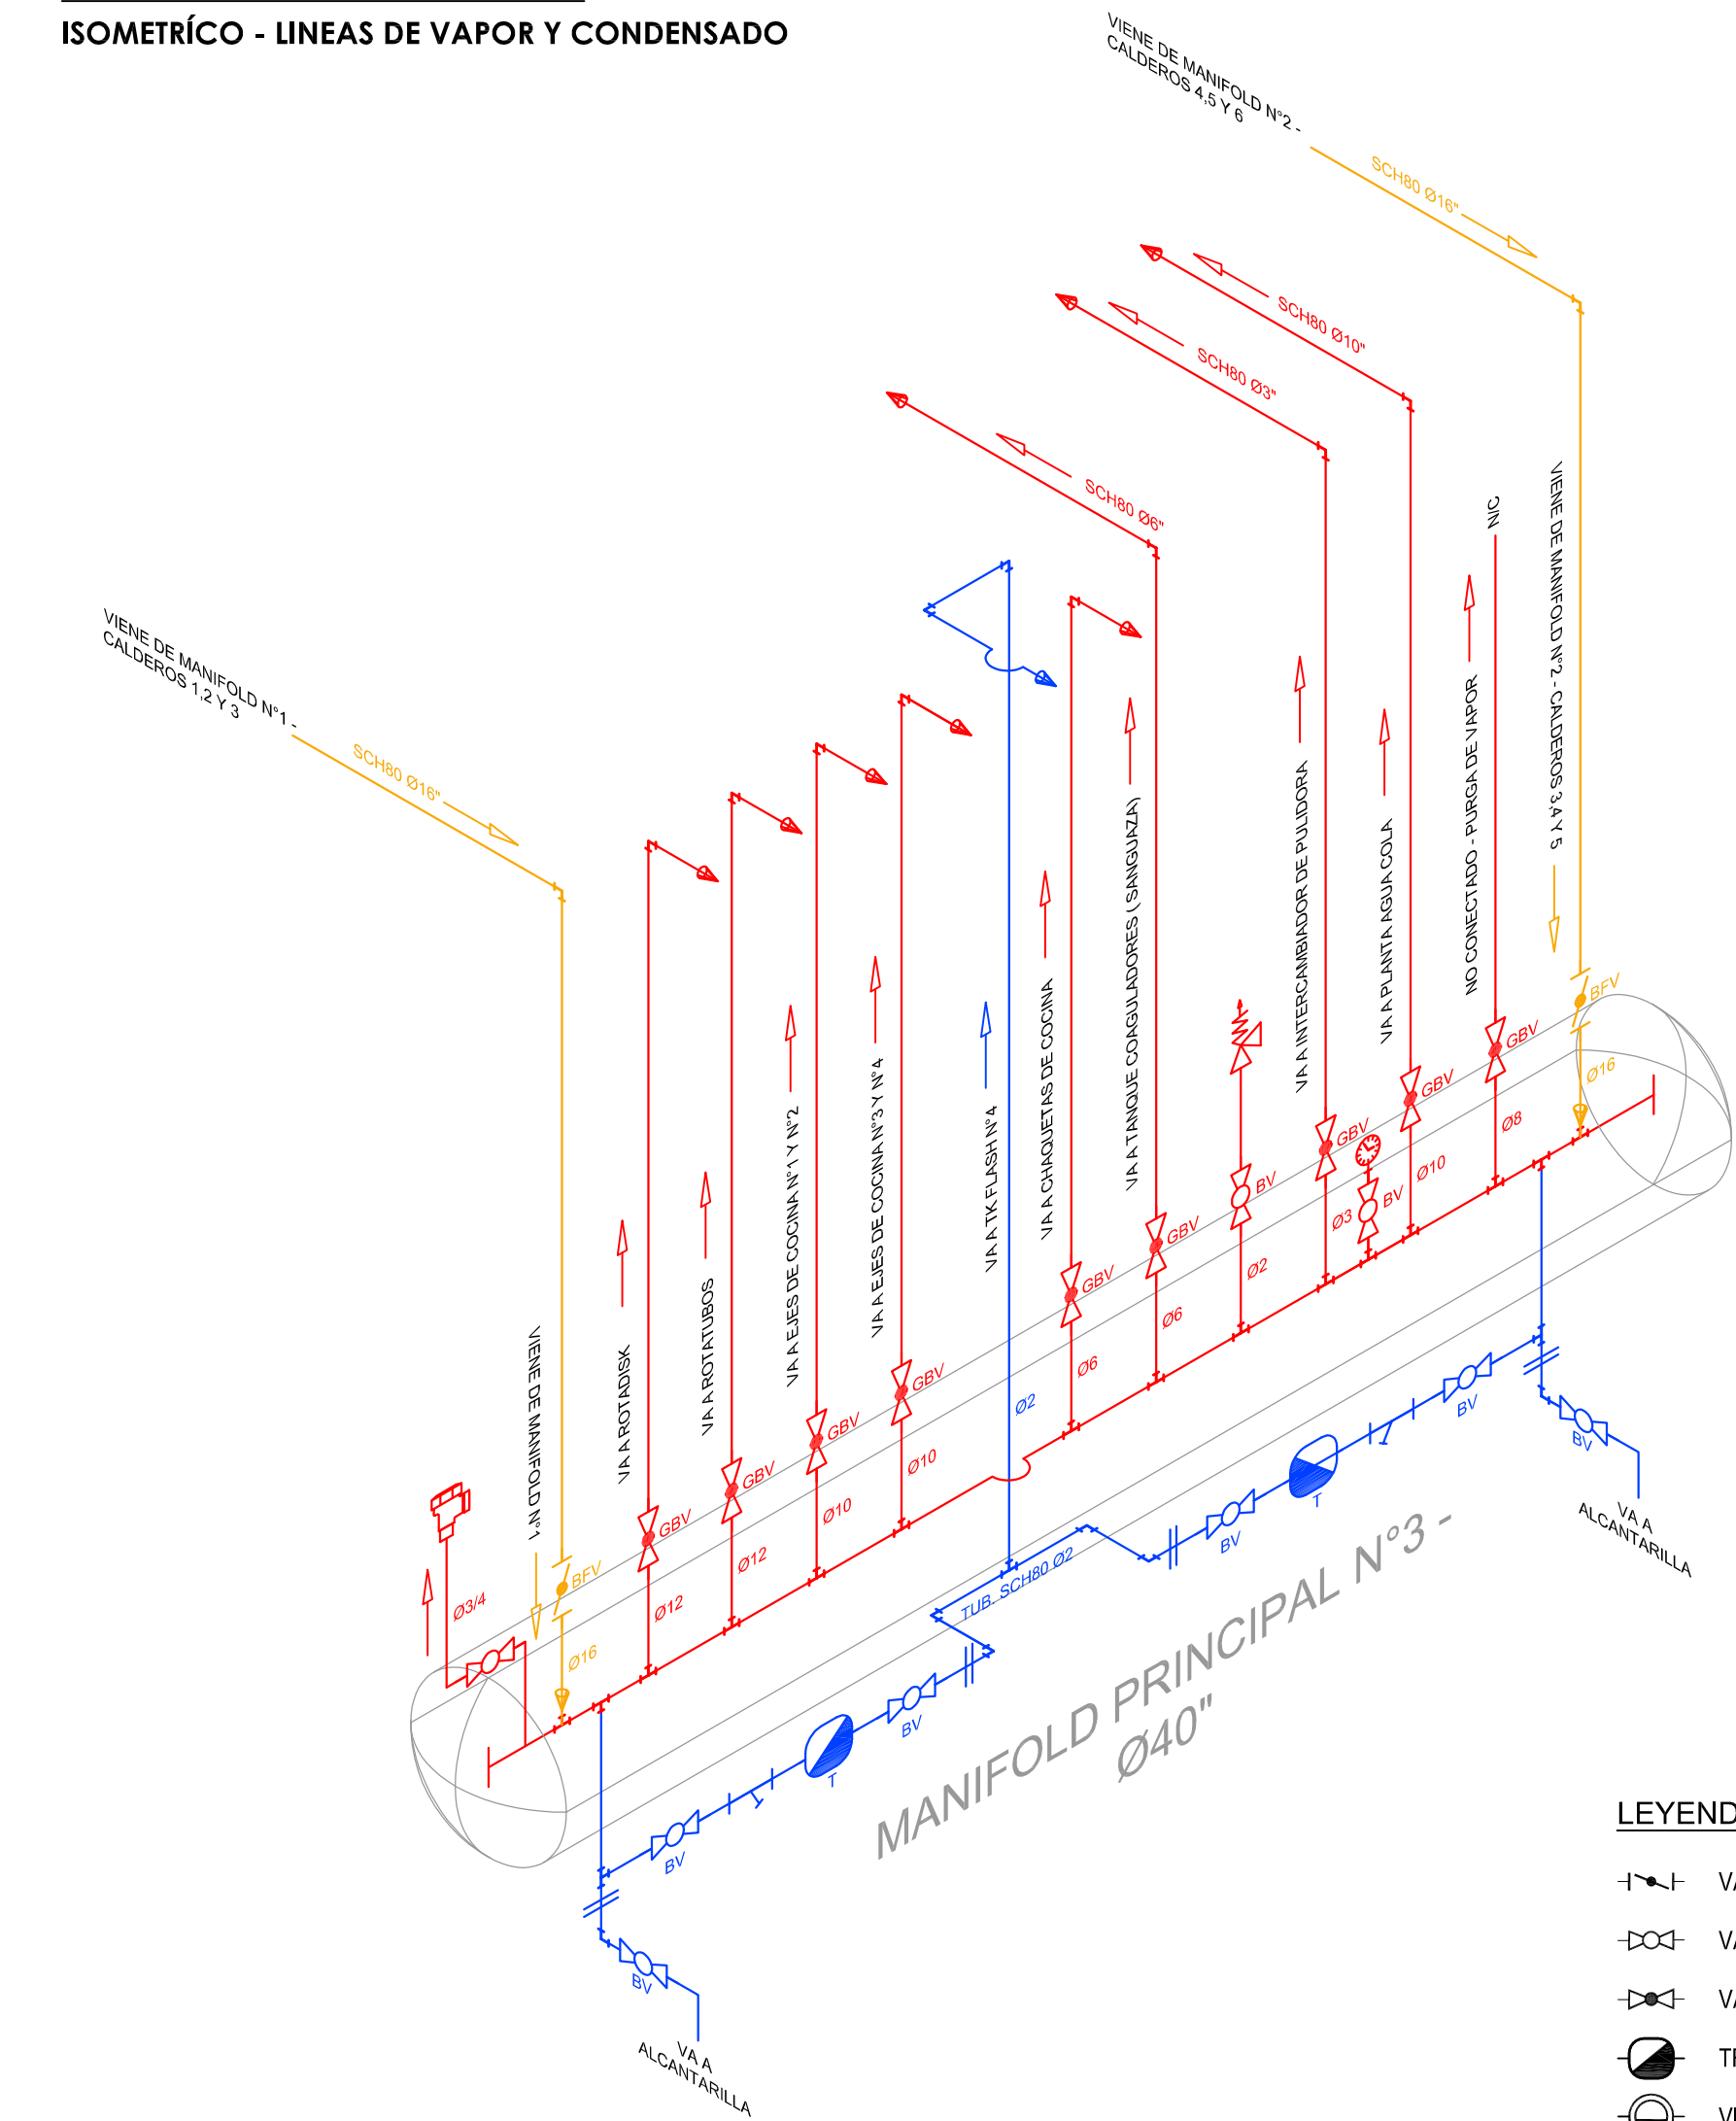

LEYENDA

- VÁLVULA MARIPOSA (BFV)
- VÁLVULA BOLA (BV)
- VÁLVULA GLOBO (GBV)
- TRAMPA DE VAPOR
- VISOR DE LIQUIDO
- VALV. DE SEGURIDAD (SV)
- VALV. TERMOSTÁTICA
- FILTRO
- BRIDA
- MANÓMETRO

LEYENDA		
ITEM	DESCRIPCIÓN	SÍMBOLO
1	LINEA DE VAPOR VIVO - 7.5 BAR	
2	LINEA DE VAPOR - 5 BAR	
3	LINEA DE CONDENSADO - 6 BAR	

					 Austral Group S.A.A. Austevoll Seafood Company	CLIENTE: AUSTRAL GROUP S.A.A. PLANTA COISHCO			
						TITULO: AUTRAL – PLANTA DE HARINA PLANO ISOMETRICO MANIFOLD DISTRIBUIDOR PRINCIPAL N°3 A PLANTA DE HARINA			
			DISEÑO POR: –	FECHA: JUNIO 2024		FORMATO A3	ESC. IND.	PLANO N.* AU–COI–VAPOR–P19	REV: A
	J.G.R	J.A.M	DIBUJADO POR: J.G.R	FECHA: JUNIO 2024					
			REVISADO POR: J.A.M.	FECHA: JUNIO 2024					
			APROBADO POR:	FECHA: JUNIO 2024					
DESCRIPCION DE REVISION	REVISADO	APROBADO							