


ADVERTENCIA: ESTE PLANO Y LA INFORMACION CONTENIDA, POR SER DE PROPIEDAD INTELECTUAL DE AUSTRAL GROUP S.A.A., SU REPRODUCCION, DIFUSION, COMERCIALIZACION O USO DE CUALQUIER TIPO, DEBERA TENER UNA AUTORIZACION ESCRITA.

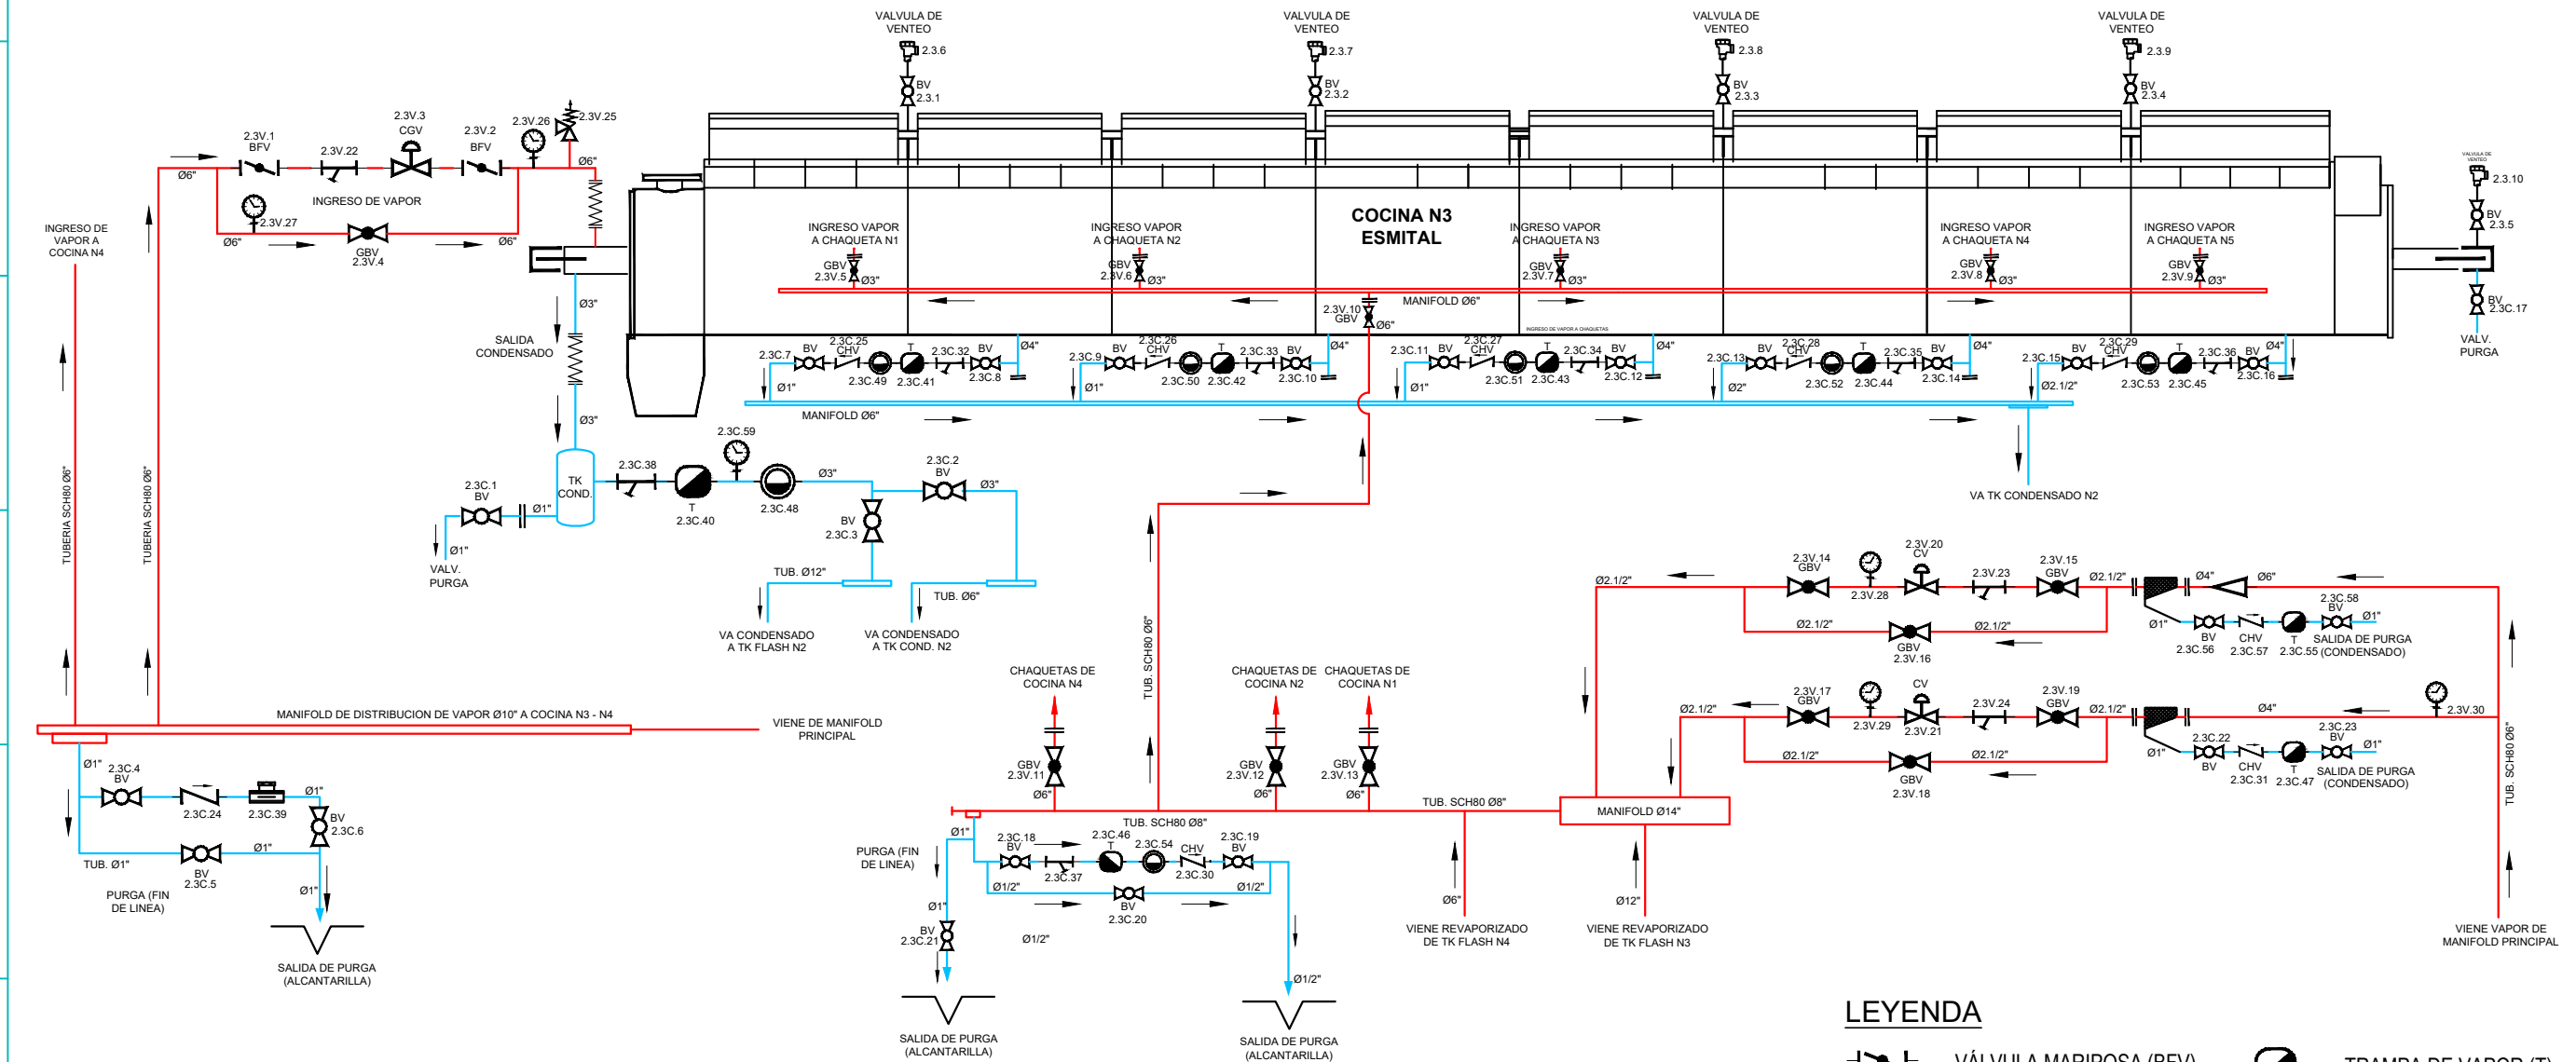

LEYENDA		
ITEM	DESCRIPCIÓN	SÍMBOLO
2	LINEA DE VAPOR - 5 BAR	
4	LINEA DE CONDENSADO - 1.5 / 2.5 BAR	

LINEA DE VAPOR Y CONDENSADO DE COCINA N3 ESMITAL

ESQUEMA DE PRINCIPIO

--	--	