


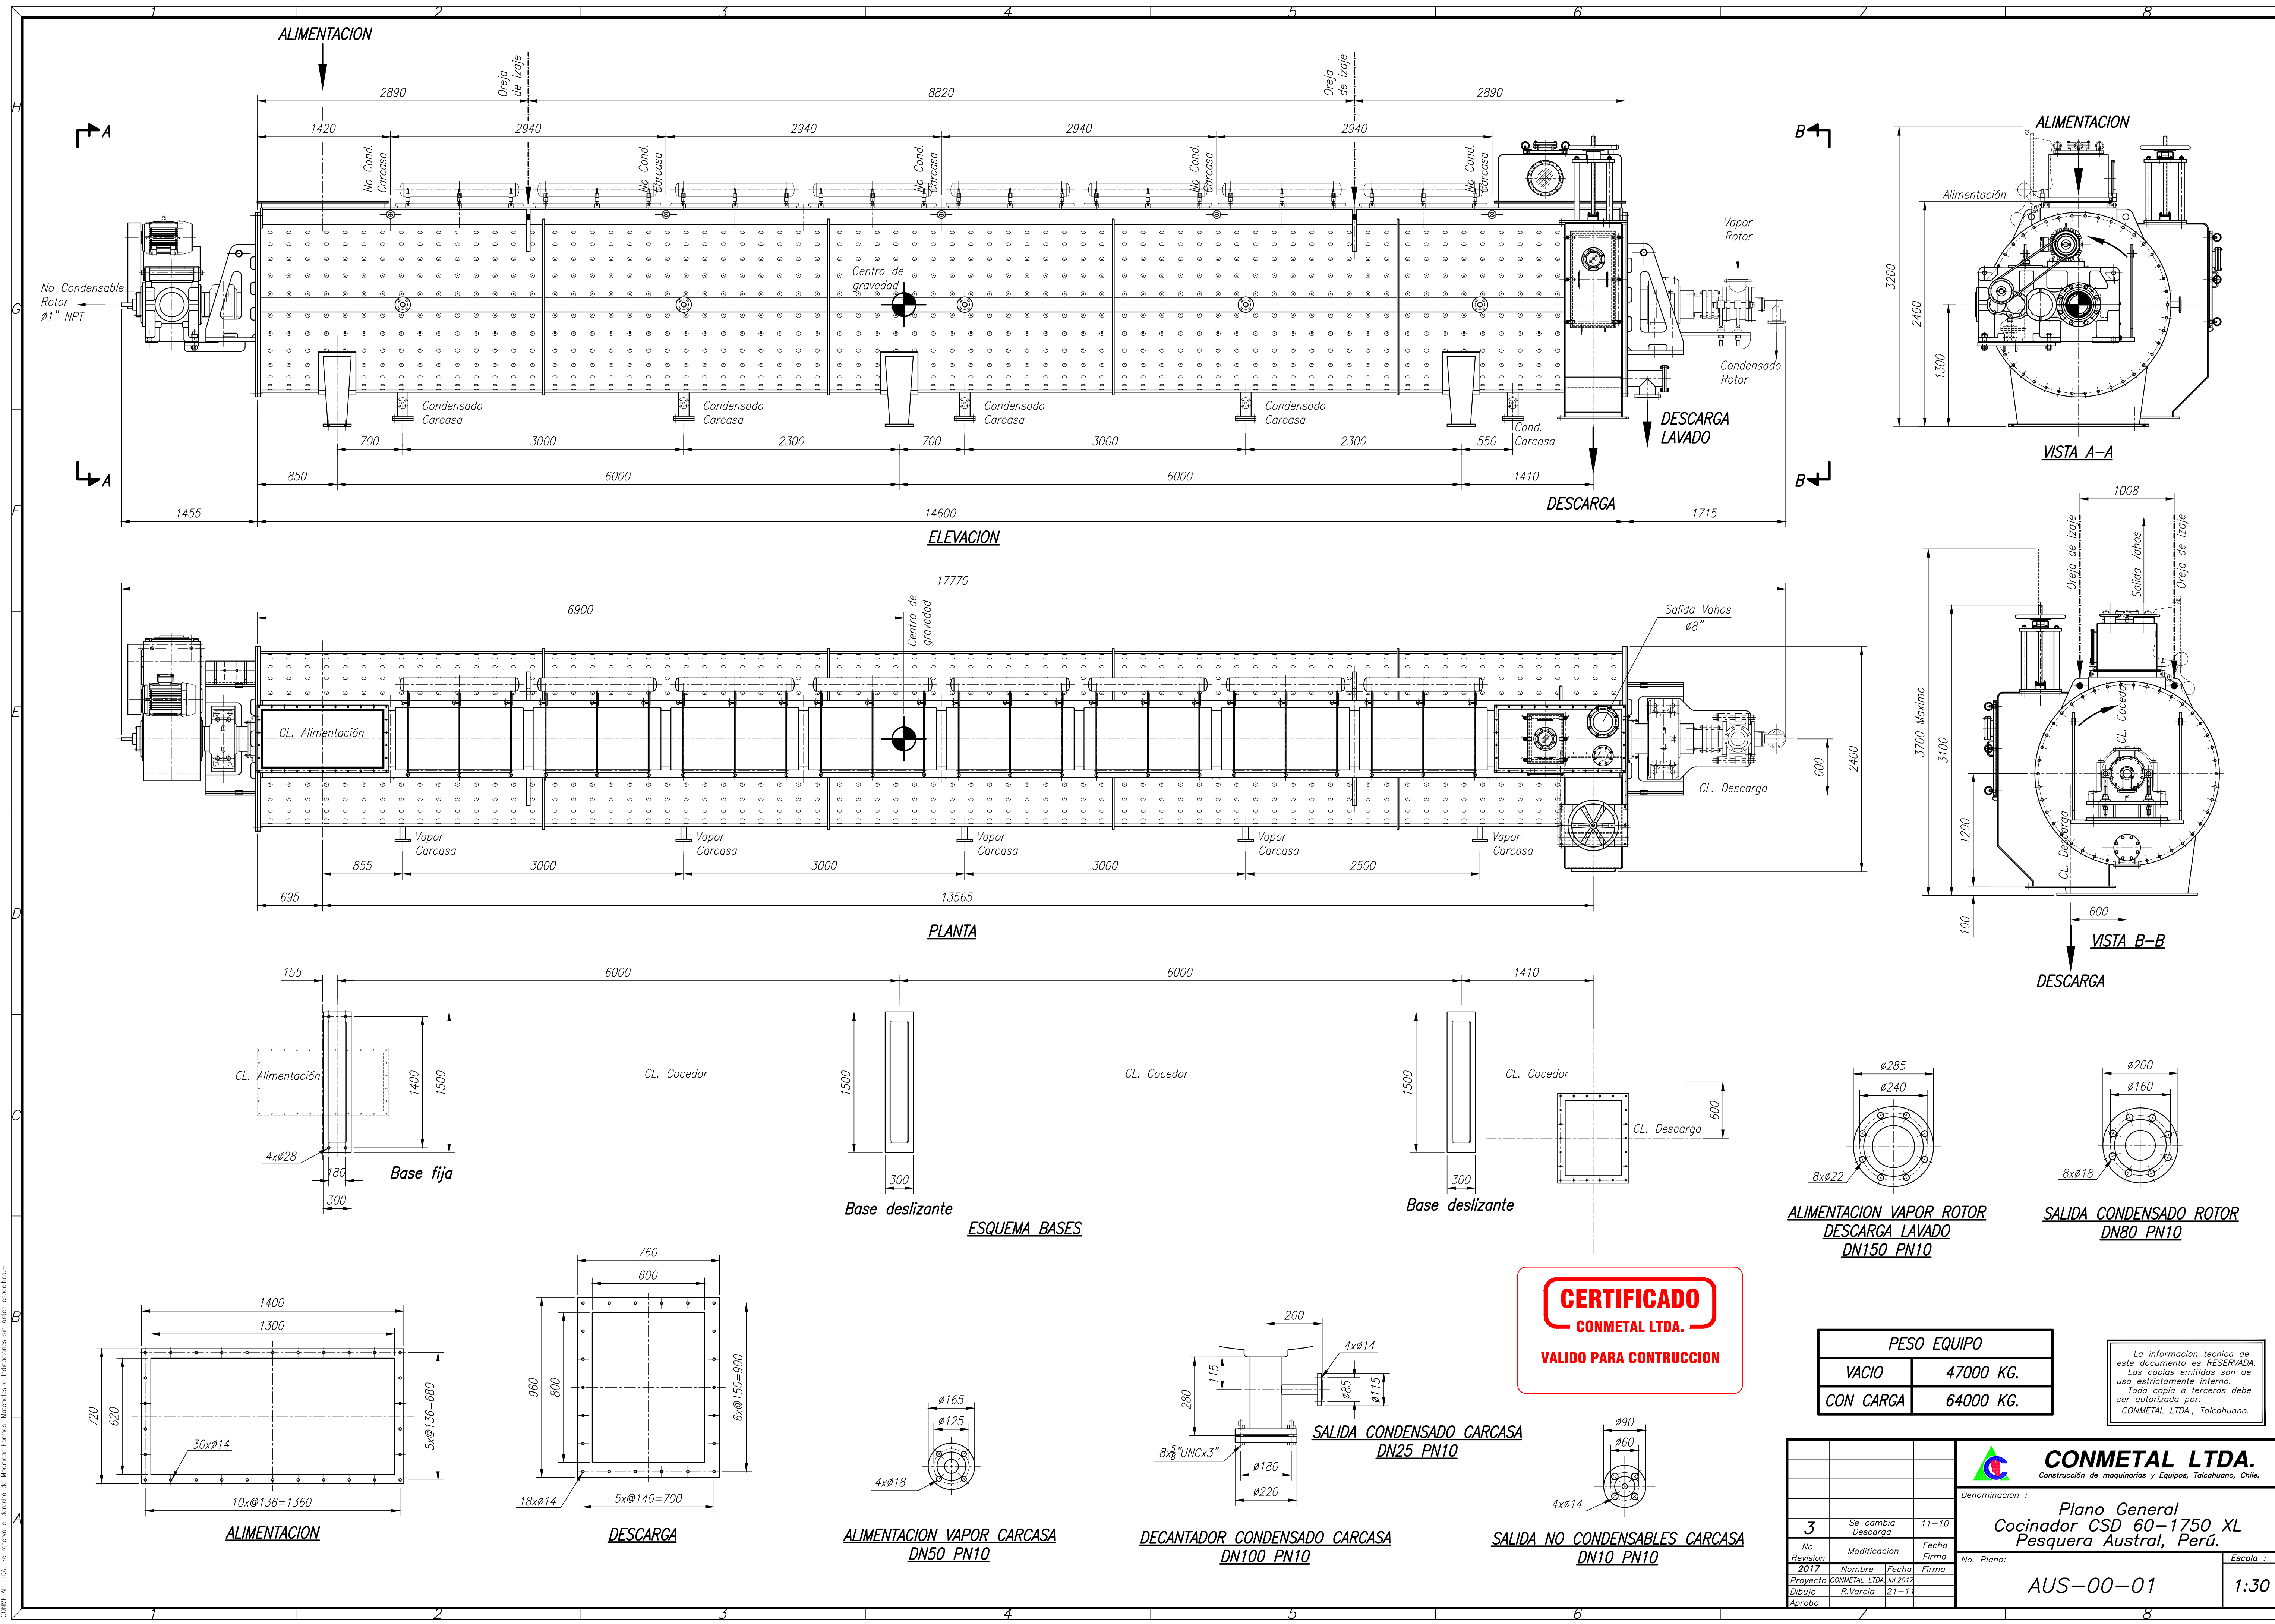

CONMETAL LTDA. Se reserva el derecho de Modificar Formas, Materiales e Indicaciones sin previo aviso.

CERTIFICADO
CONMETAL LTDA.
VALIDO PARA CONTRUCCION

PESO EQUIPO	
VACIO	47000 KG.
CON CARGA	64000 KG.

La informacion tecnica de este documento es RESERVADA. Las copias emitidas son de uso estrictamente interno. Toda copia a terceros debe ser autorizada por: CONMETAL LTDA., Talcahuano.

CONMETAL LTDA.			
Construcción de maquinarias y Equipos, Talcahuano, Chile.			
Denominación : Plano General Cocinador CSD 60-1750 XL Pesquera Austral, Perú.			
No. Plano:		Escala :	
AUS-00-01		1:30	
3	Se cambia Descarga	11-10	
No. Revision	Modificación	Fecha	Firma
2017	Nombre	Fecha	Firma
Proyecto	CONMETAL LTDA.	Jul.2017	
Dibujo	R.Varela	21-11	
Aproba			