




ADVERTENCIA: ESTE PLANO Y LA INFORMACION CONTENIDA, POR SER PROPIEDAD INTELECTUAL AUSTRAL GROUP S.A.A., SU REPRODUCCION, DIFUSION, COMERCIALIZACION O USO CUALQUIER TIPO, DEBERA TENER UNA AUTORIZACION ESCRITA.

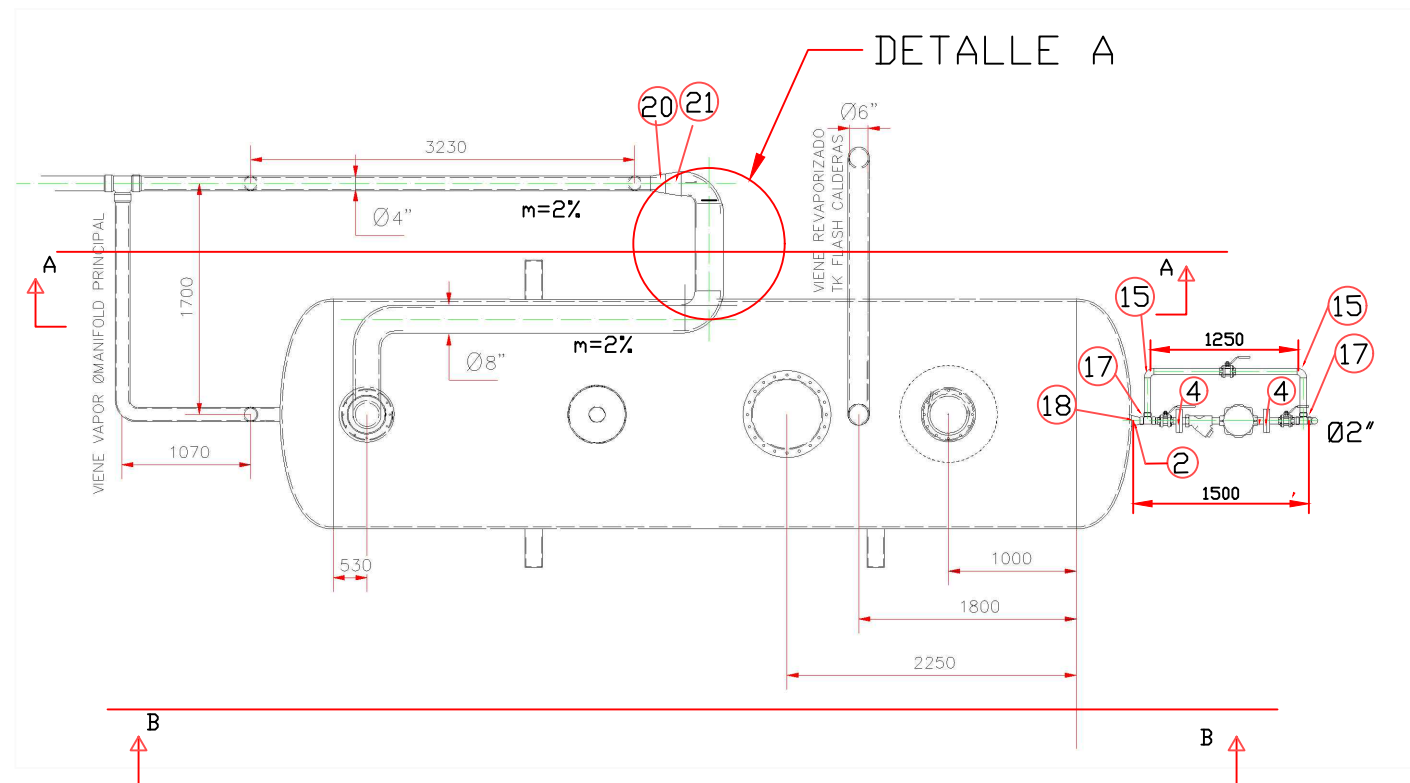


VISTA DE PLANTA

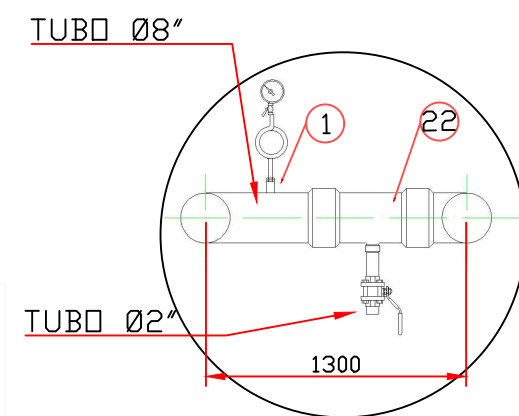


VISTA DETALLE A

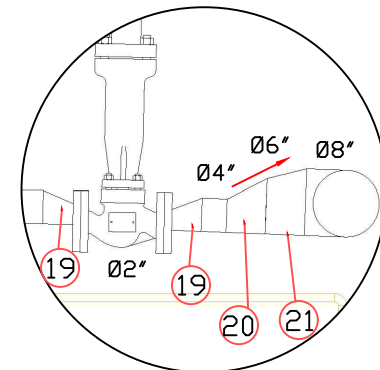

VISTA DETALLE B

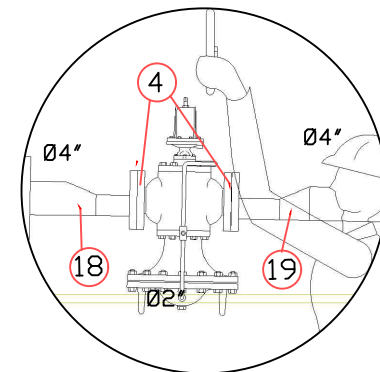

VISTA DETALLE C

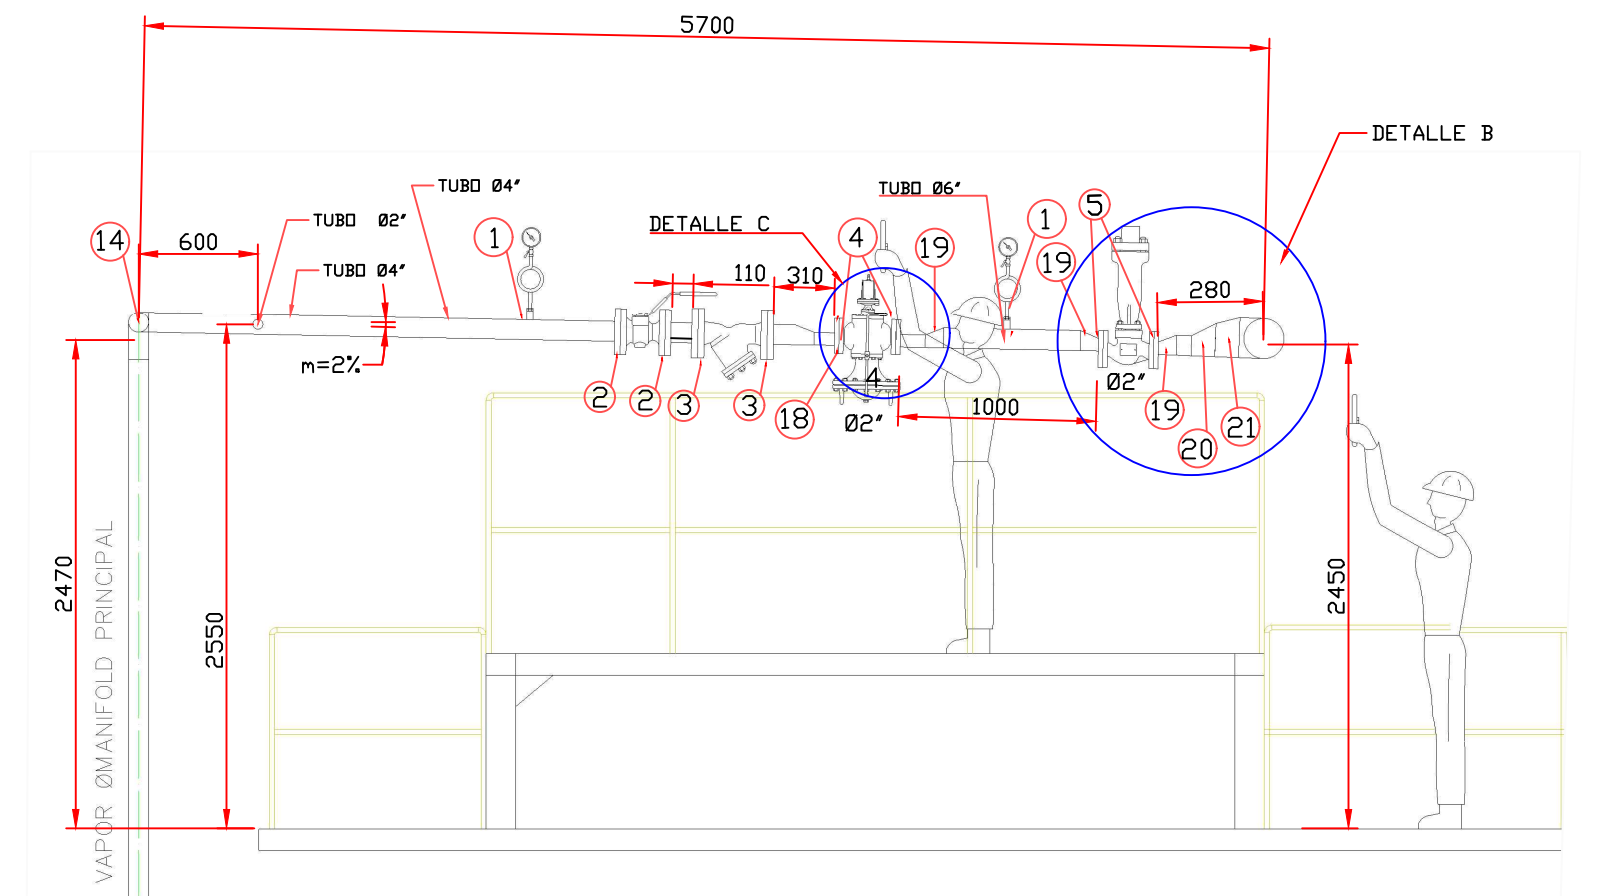


VISTA LATERAL

A - A

ITEM	POSICION	CODIGO	DESCRIPCION	CANTIDAD
1	P1	VEMFA	NIPLE Ø1/2" x2 y UNION ENROSCABLE DE 1/2" de 180º	1
2	P2	M40Si2	BRIDAS ACERO ASMT A105, CLASE 150 - MED de 4" a 9", CON NUMERO DE HUECOS 3/4" [8]	2
3	P3	FIG34	BRIDAS ACERO ASMT A105, CLASE 150 - MED de 4" a 9", CON NUMERO DE HUECOS 3/4" [8]	2
4	P4	25P	BRIDAS ACERO ASMT A105, CLASE 150 - MED de 2" a 9", CON NUMERO DE HUECOS 7/8" [8]	2
5	P5	LEA33	BRIDAS ACERO ASMT A105, CLASE 150 - MED de 4" a 9", CON NUMERO DE HUECOS 3/4" [8]	2
6	P8	BSAIT 4"	BRIDAS ACERO ASMT A105, CLASE 150 - MED de 4" a 9", CON NUMERO DE HUECOS 3/4" [8]	2
7	P14	M1052	NIPLE ENROSCABLE DE DIAM. Ø2"x115mm	1
8	P16	FT14	NIPLE ENROSCABLE DE DIAM. Ø2"x130mm	1
9	P15	FIG12	NIPLE ENROSCABLE DE DIAM. Ø2"x110mm	1
10	P17	EL2270	NIPLE ENROSCABLE DE DIAM. Ø2"x180mm	1
11	P18	BSAIT 1"	BRIDAS ACERO ASMT A105, CLASE 150 - MED de 1" a 4-1/2", CON NUMERO DE HUECOS 3/4" [8]	2
12		-	PERNOS DE 3/4" x3"	128
13		-	PERNOS DE 7/8" x3"	32
14		-	CODO DE 4"	2
15		-	CODO DE 2"	6
16		-	COLECCIÓN "T" DE 4"	2
17		-	COLECCIÓN "T" DE 2"	2
18		-	TUBO REDUCCION DE 4" a 2"	2
19		-	TUBO REDUCCION DE 2" a 6"	2
20		-	TUBO REDUCCION DE 4" a 6"	1
21		-	TUBO REDUCCION DE 6" a 8"	1
22		-	CONEXION "T" DE REDUCCION DE 8" a 2"	

PLANO DE VISTA ELEVACION Y PLANTA DE CONEXION DE TANQUE DESAIREADOR - LINEA DE VAPOR

Escala: S/E

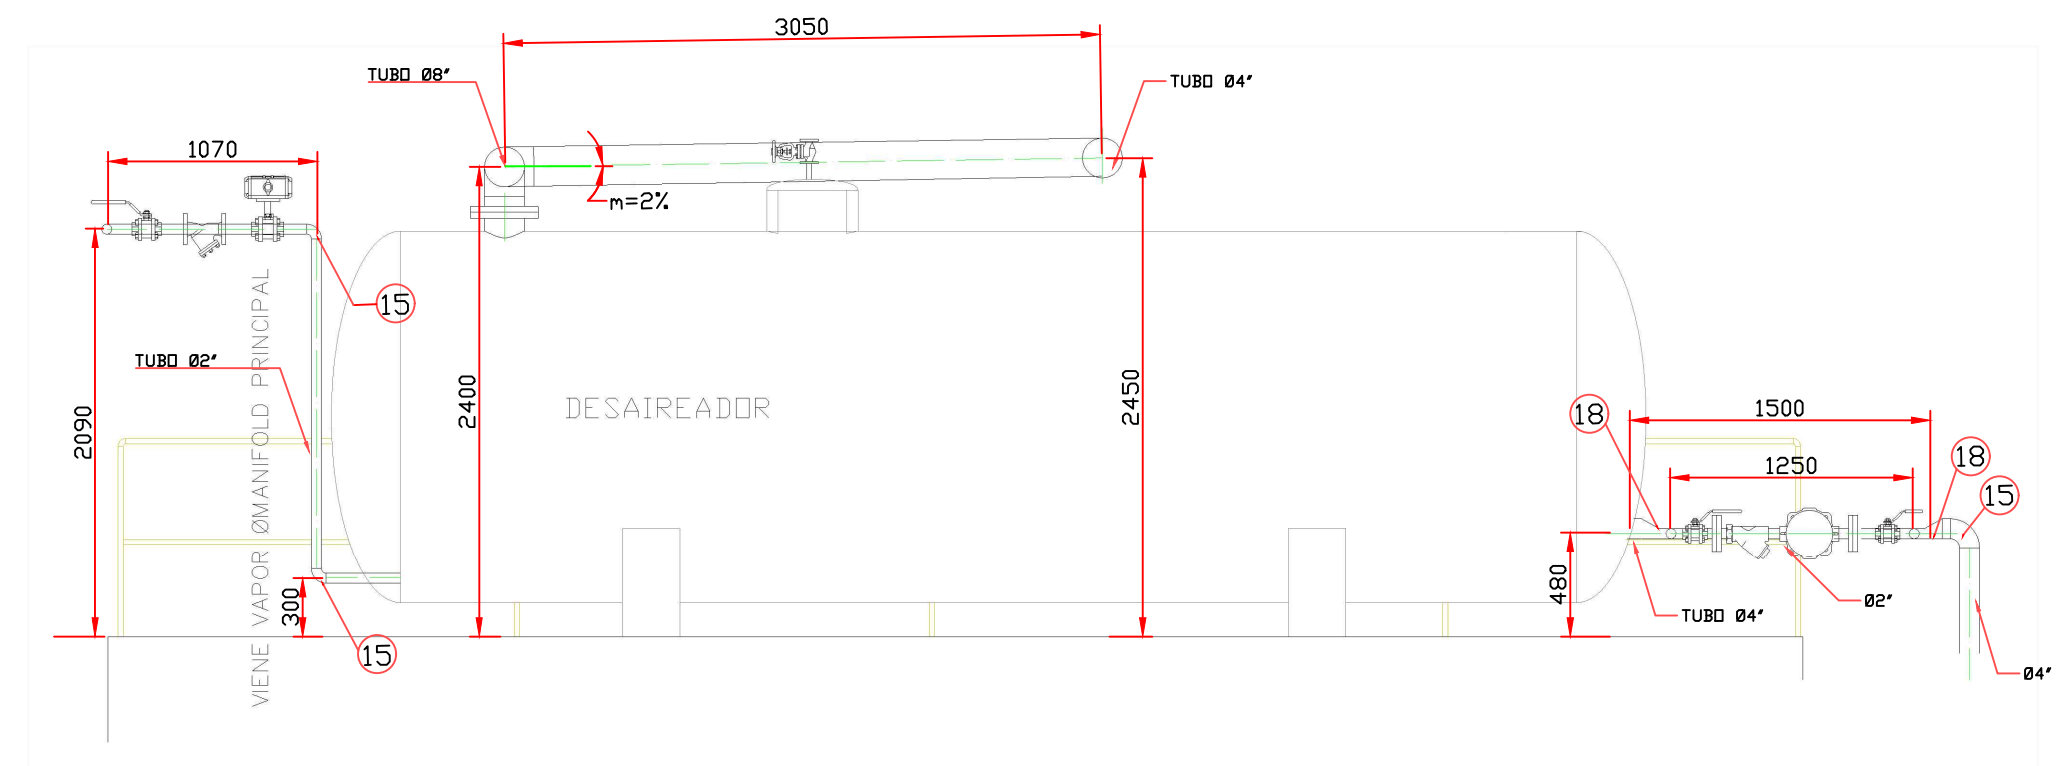

VISTA LATERAL

B - B

[illegible]