




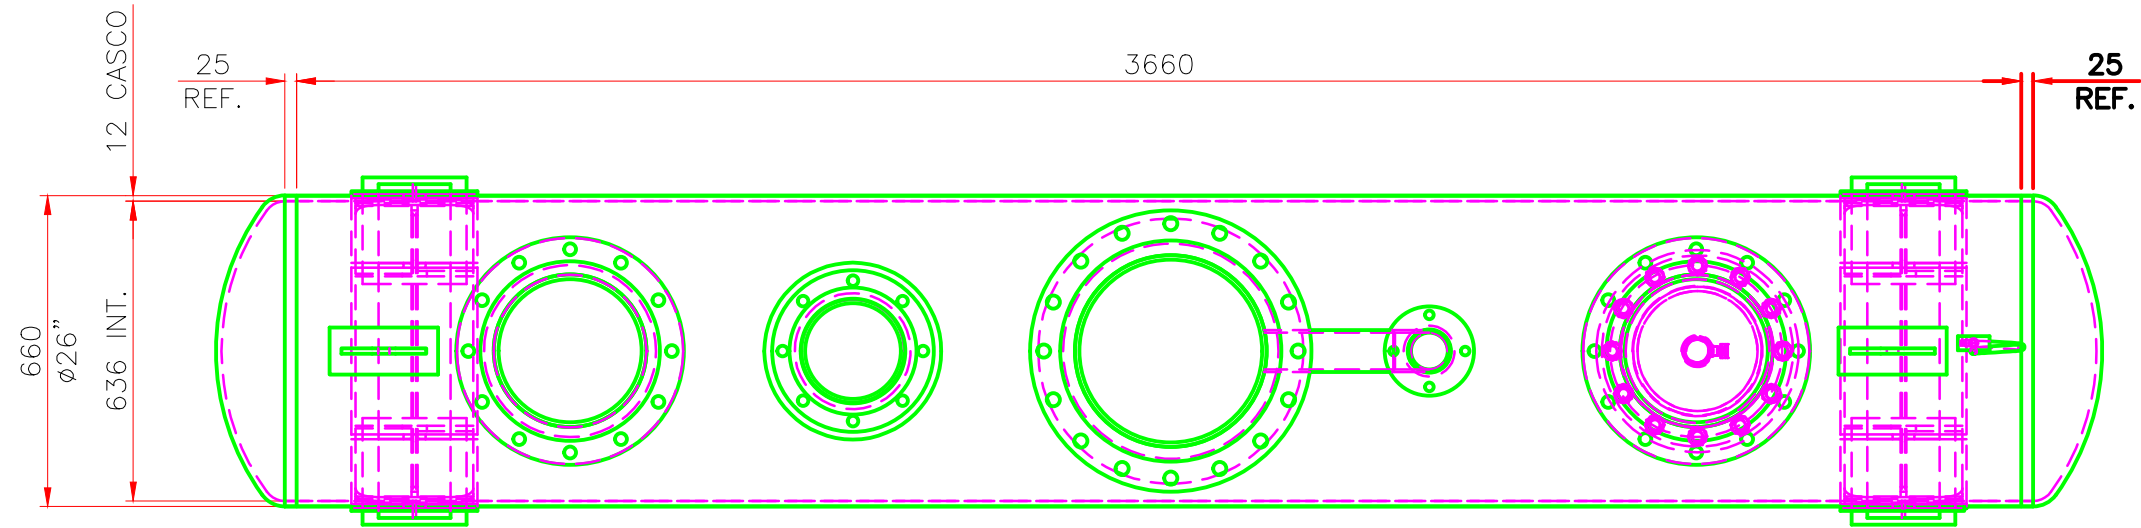




VISTA DE PLANTA
ESC. 1:16

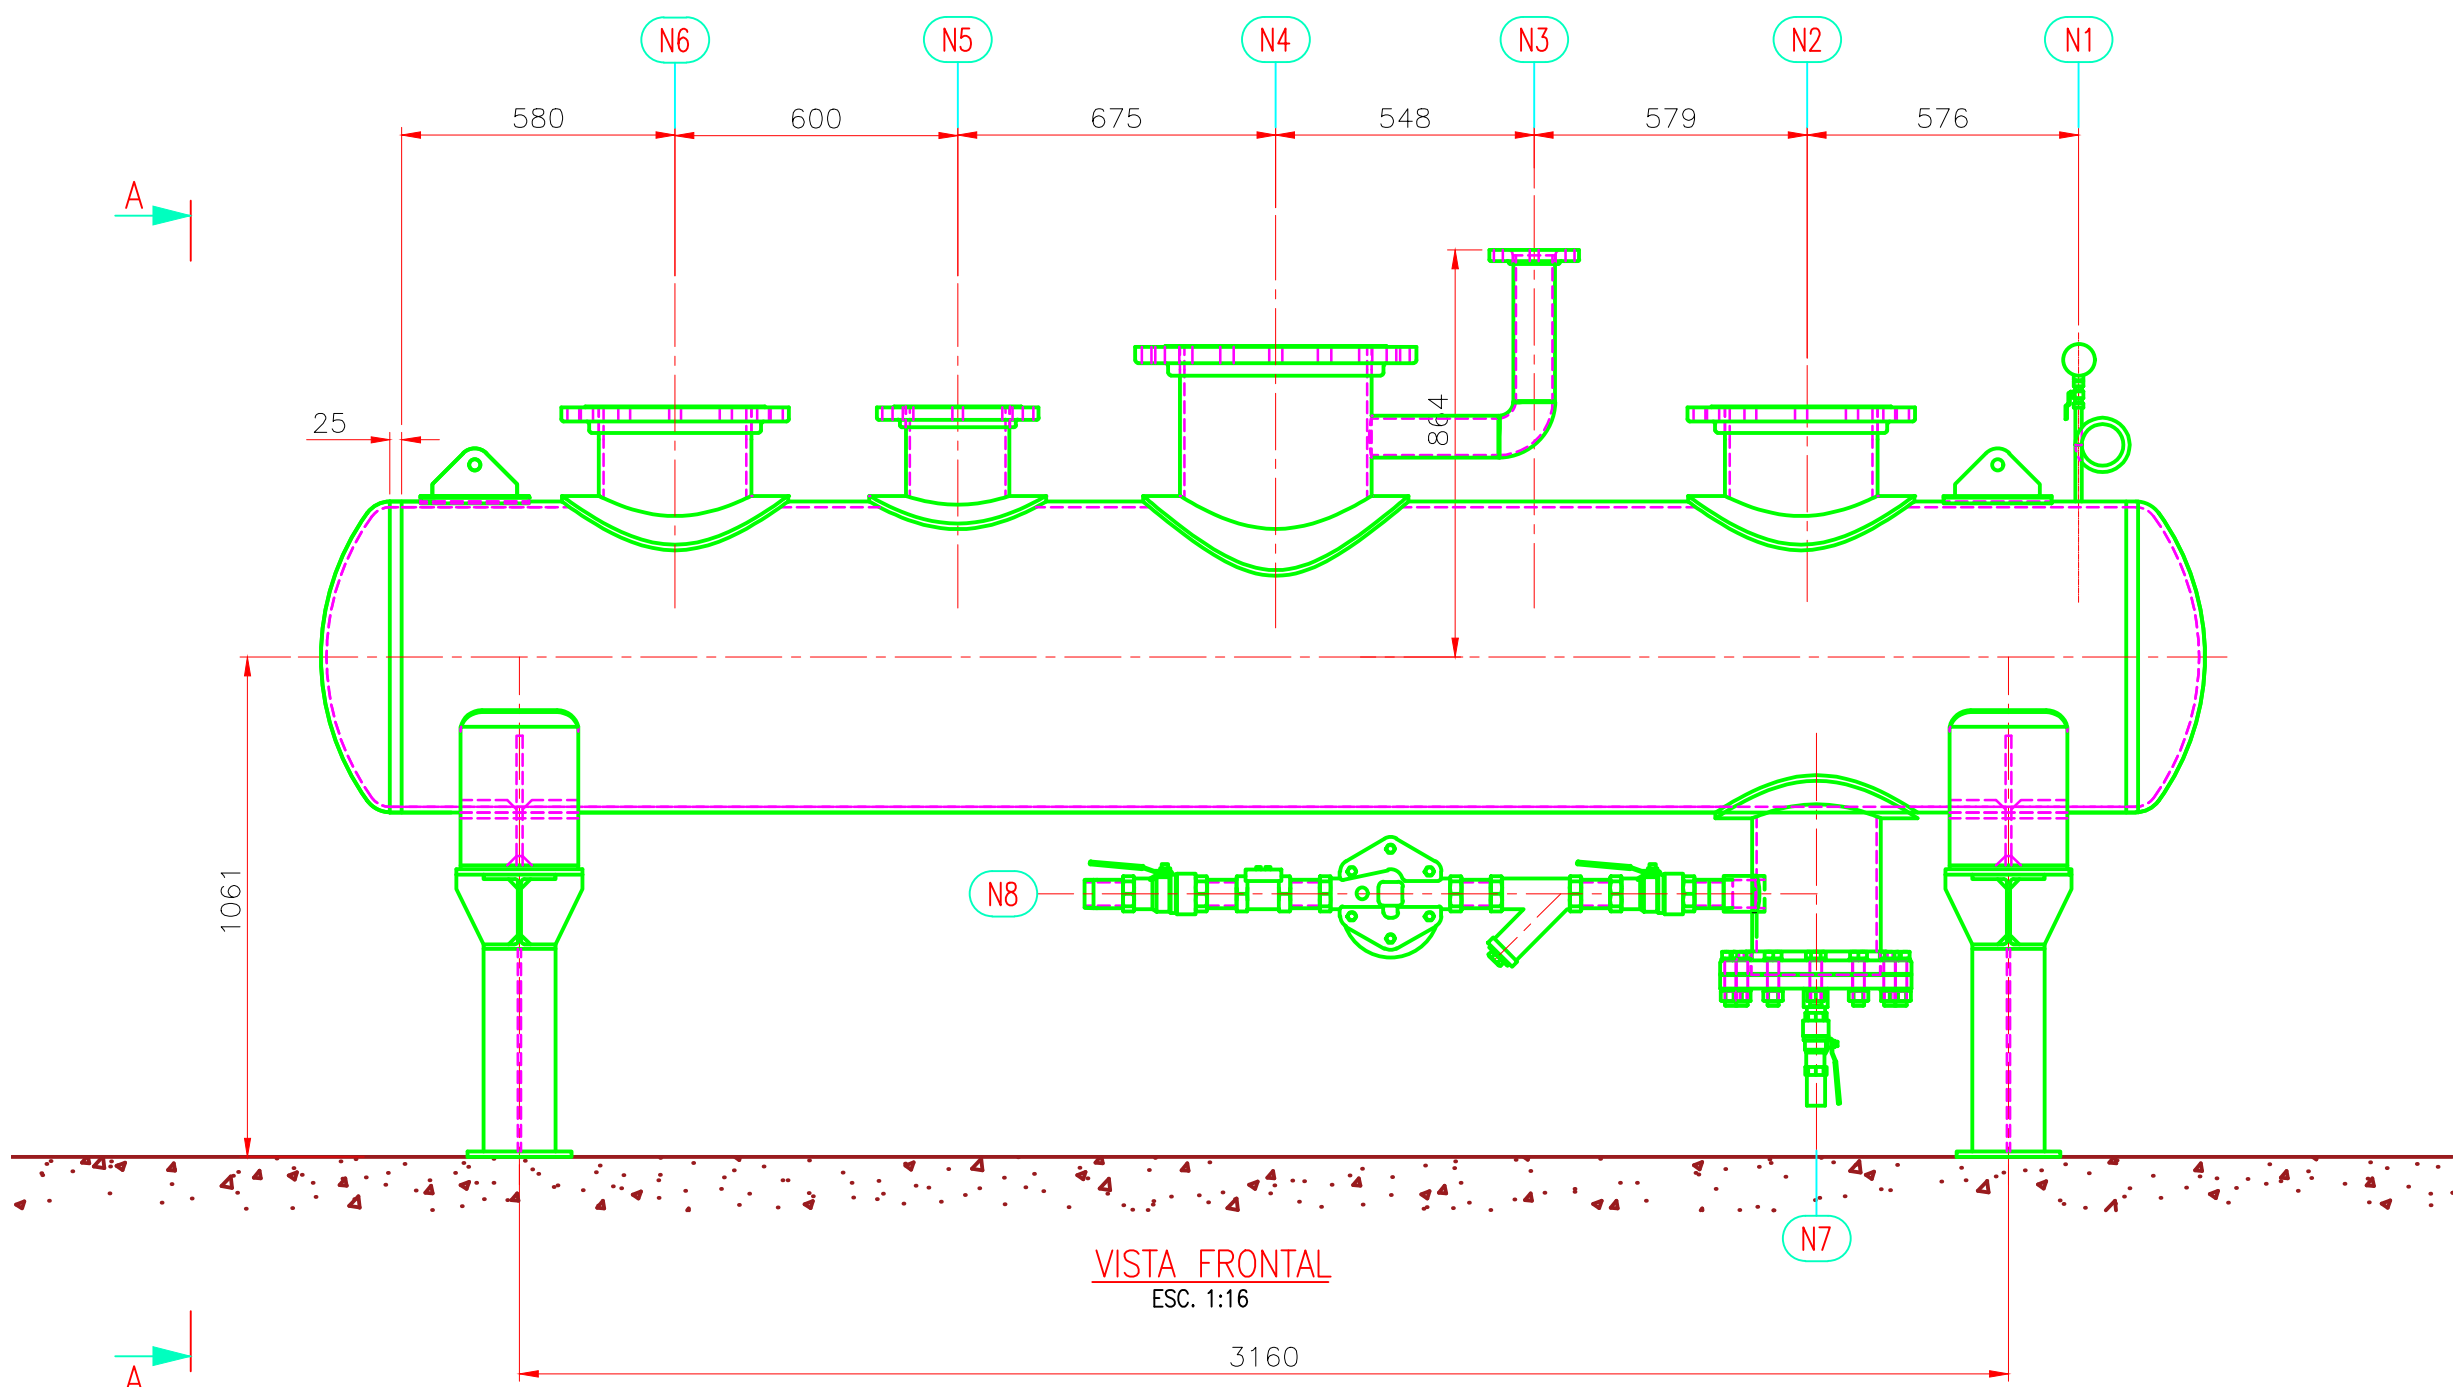


VISTA FRONTAL
ESC. 1:16

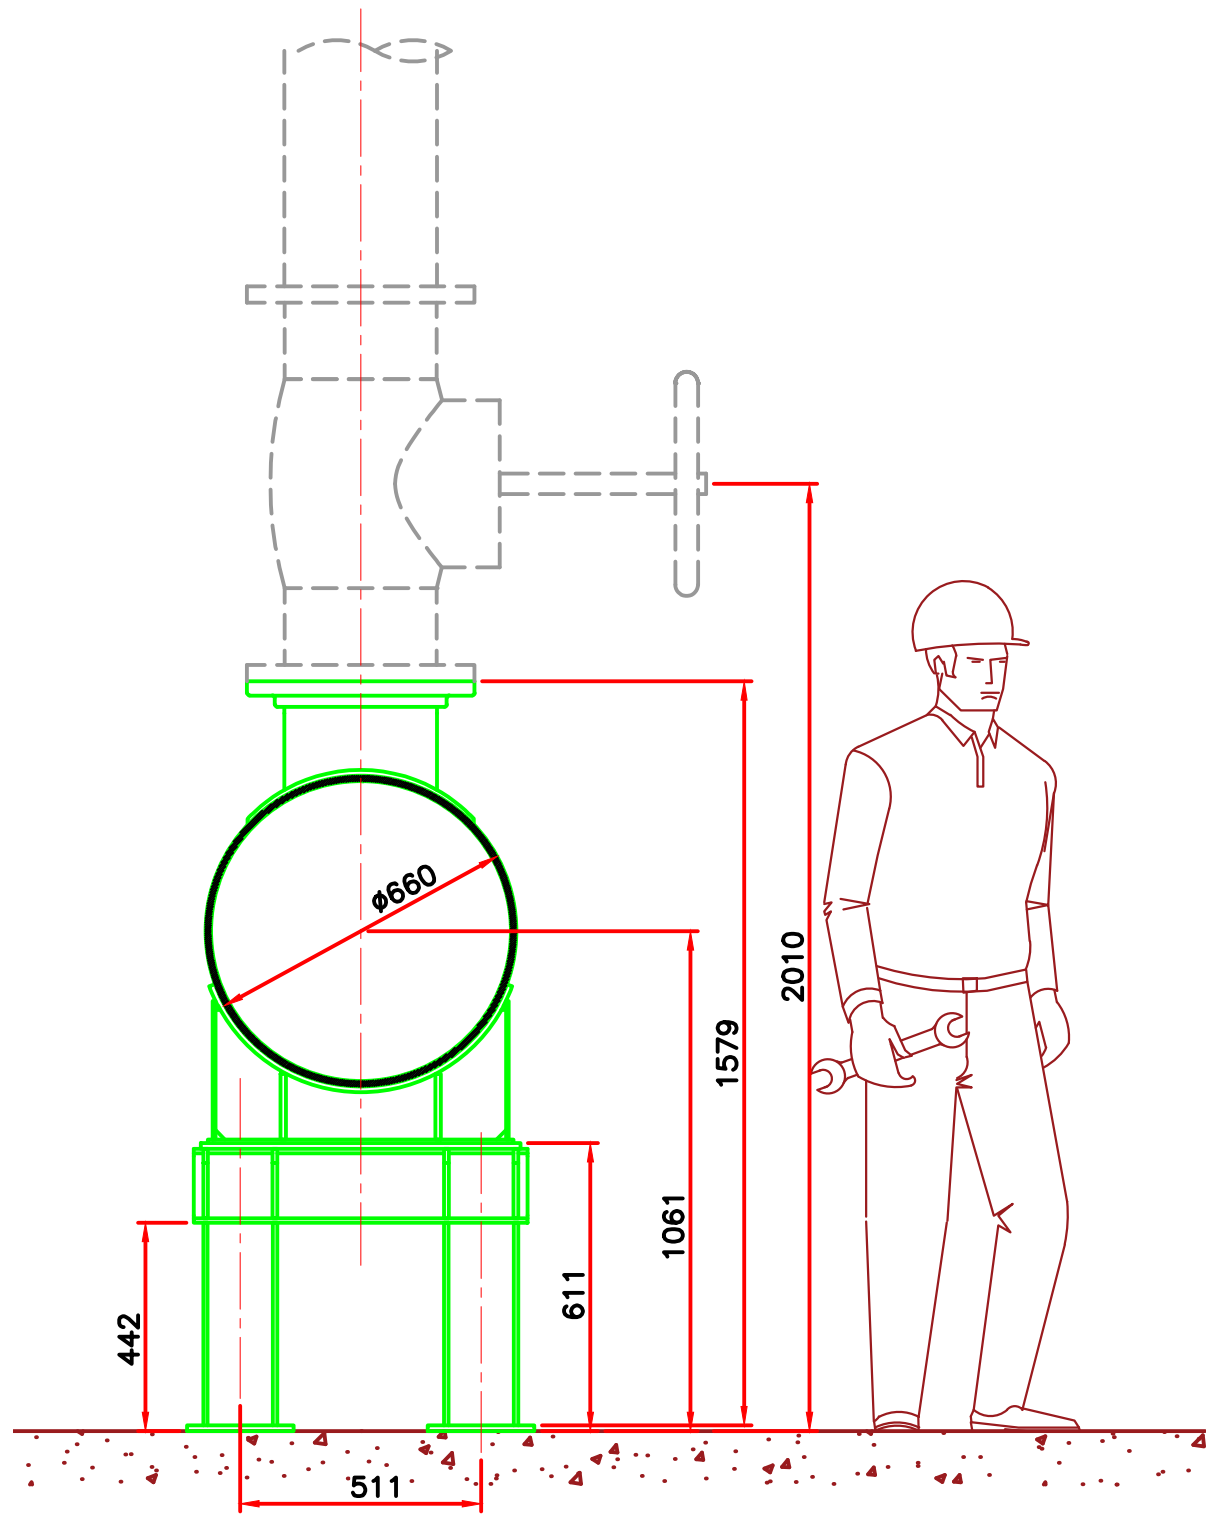


VISTA A-A
ESC. 1:16

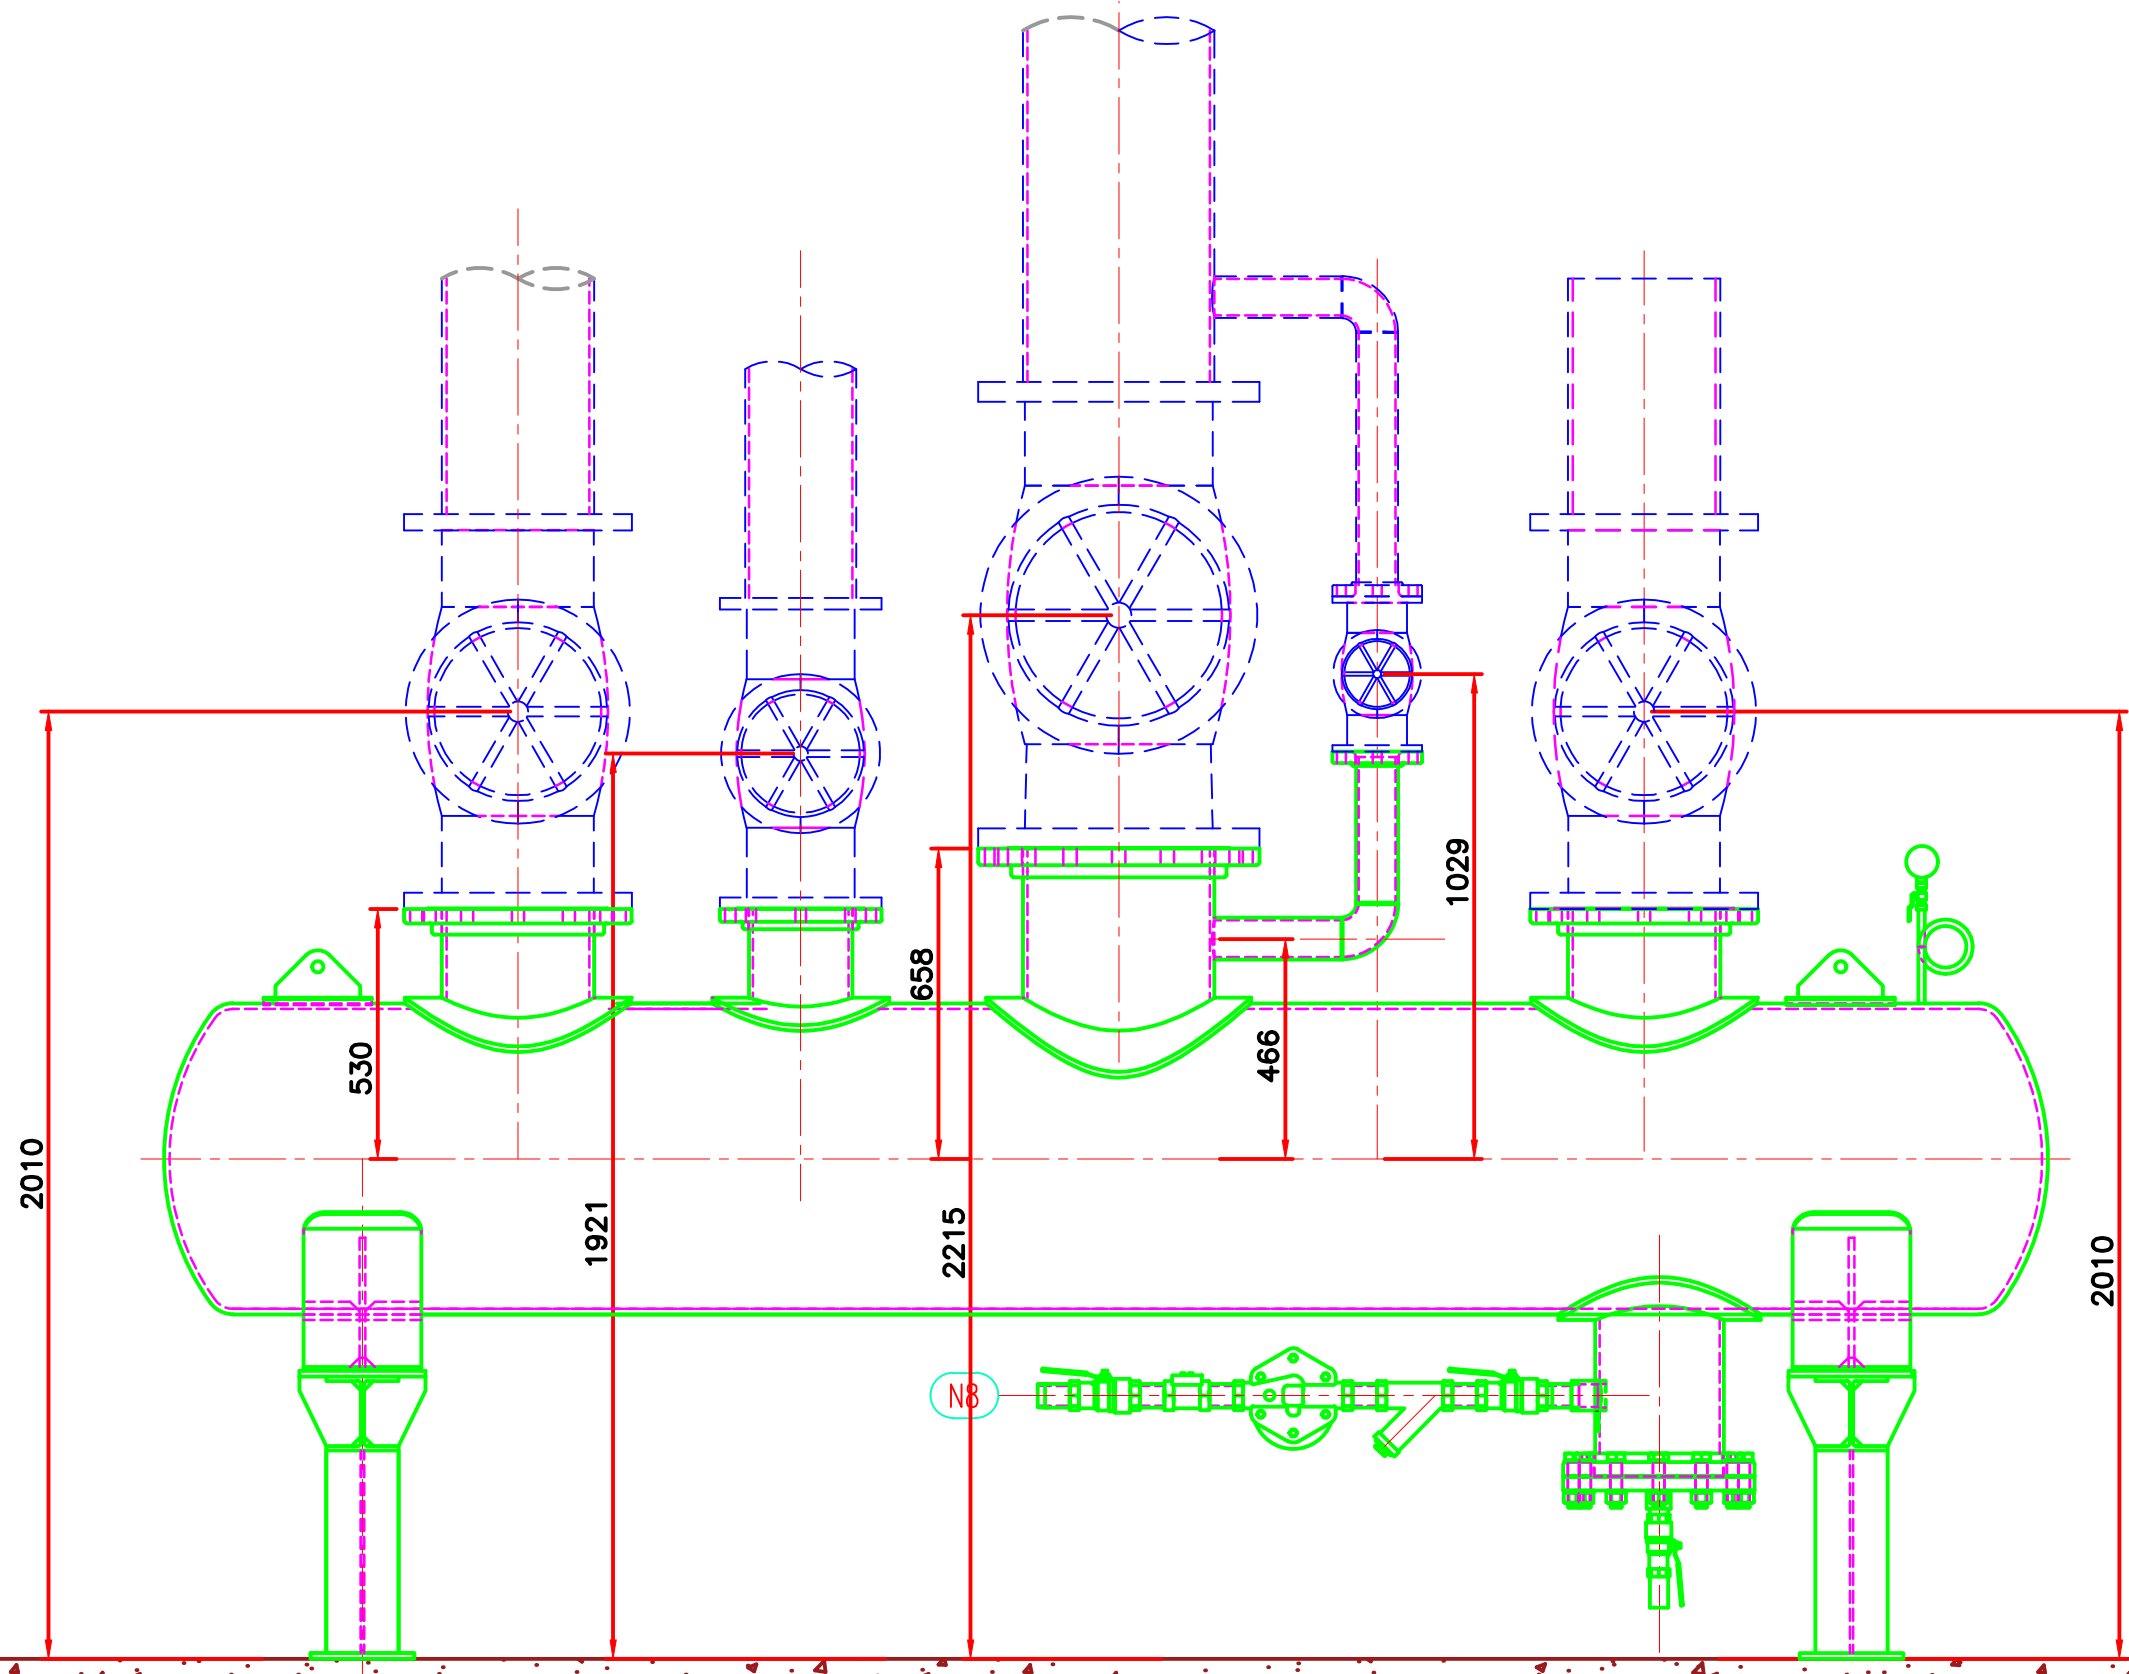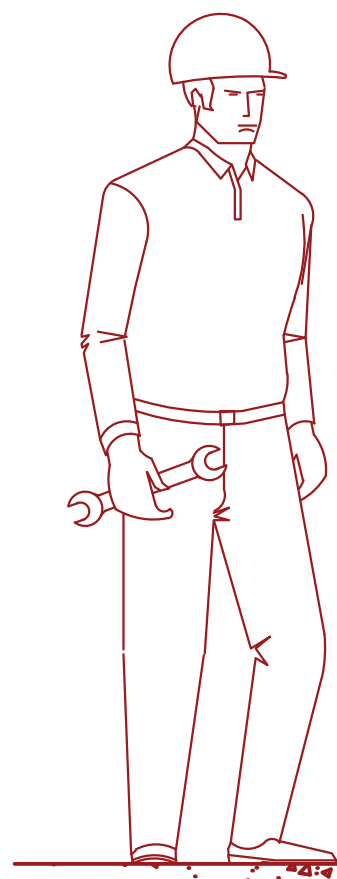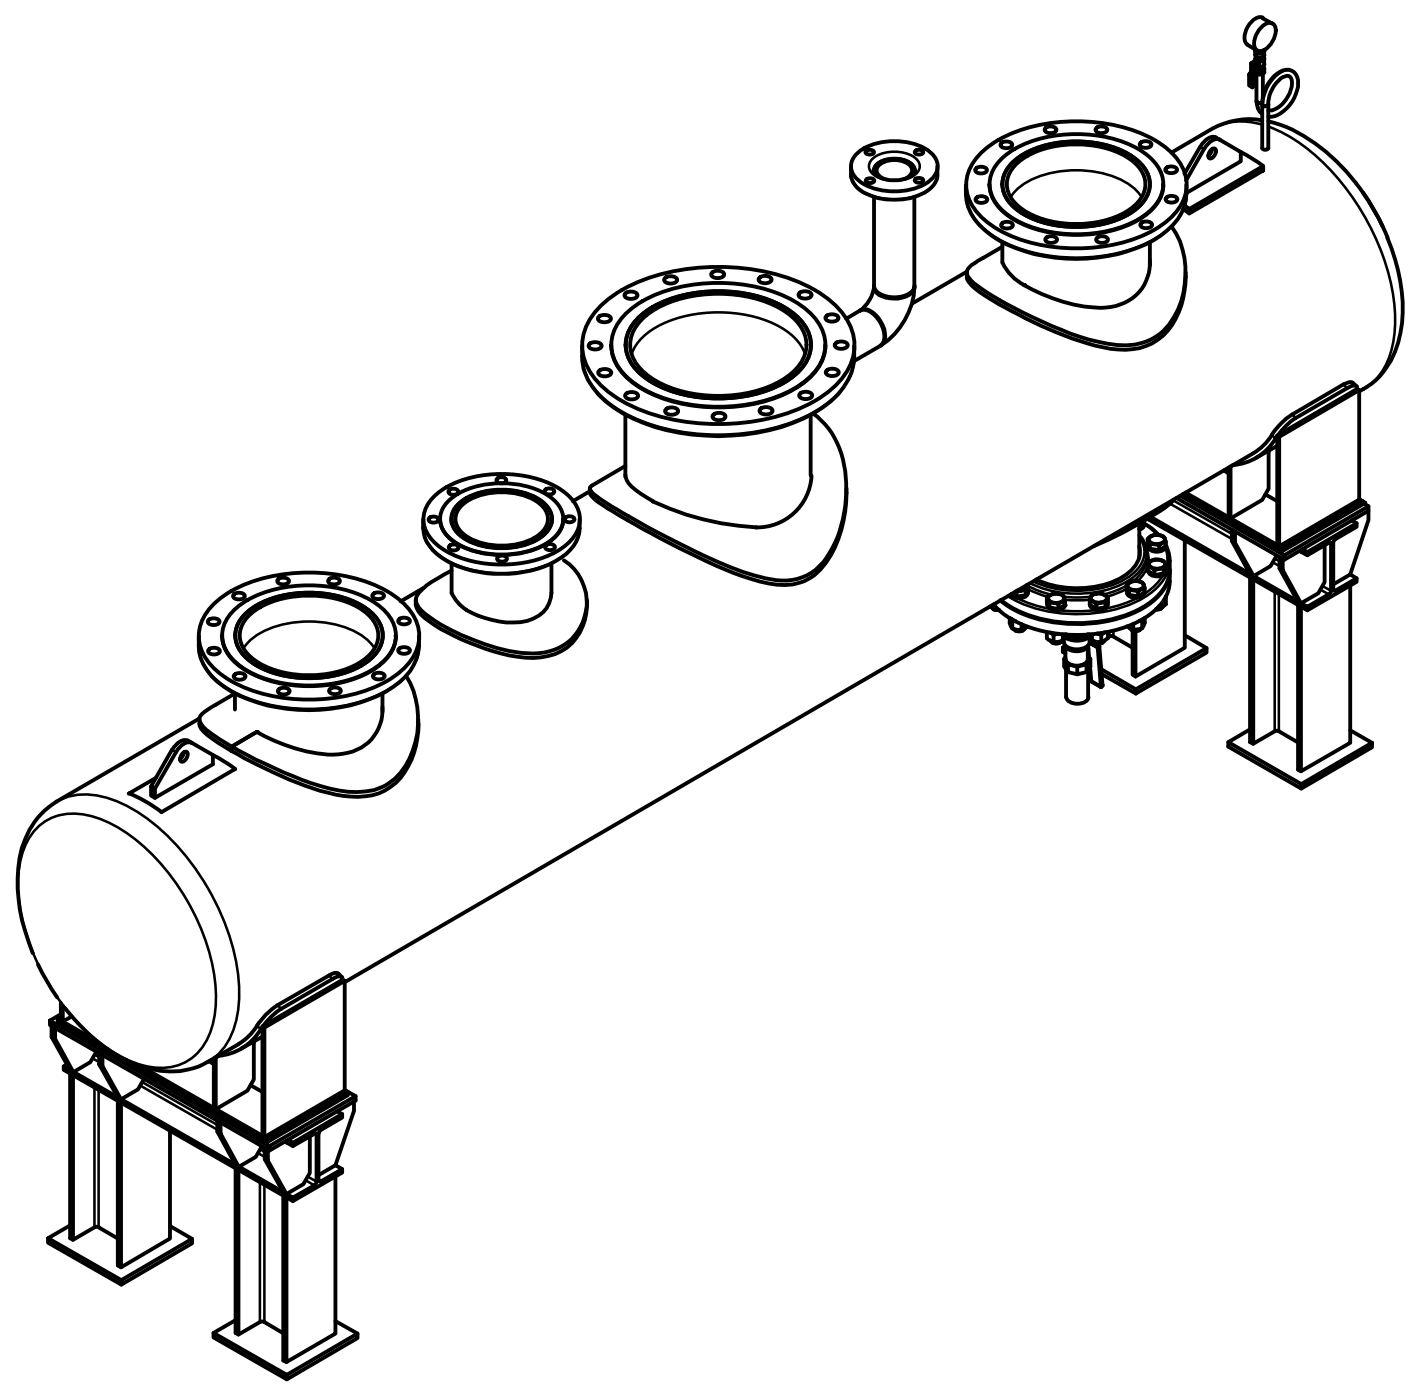

VISTA FRONTAL
ESC. 1:16

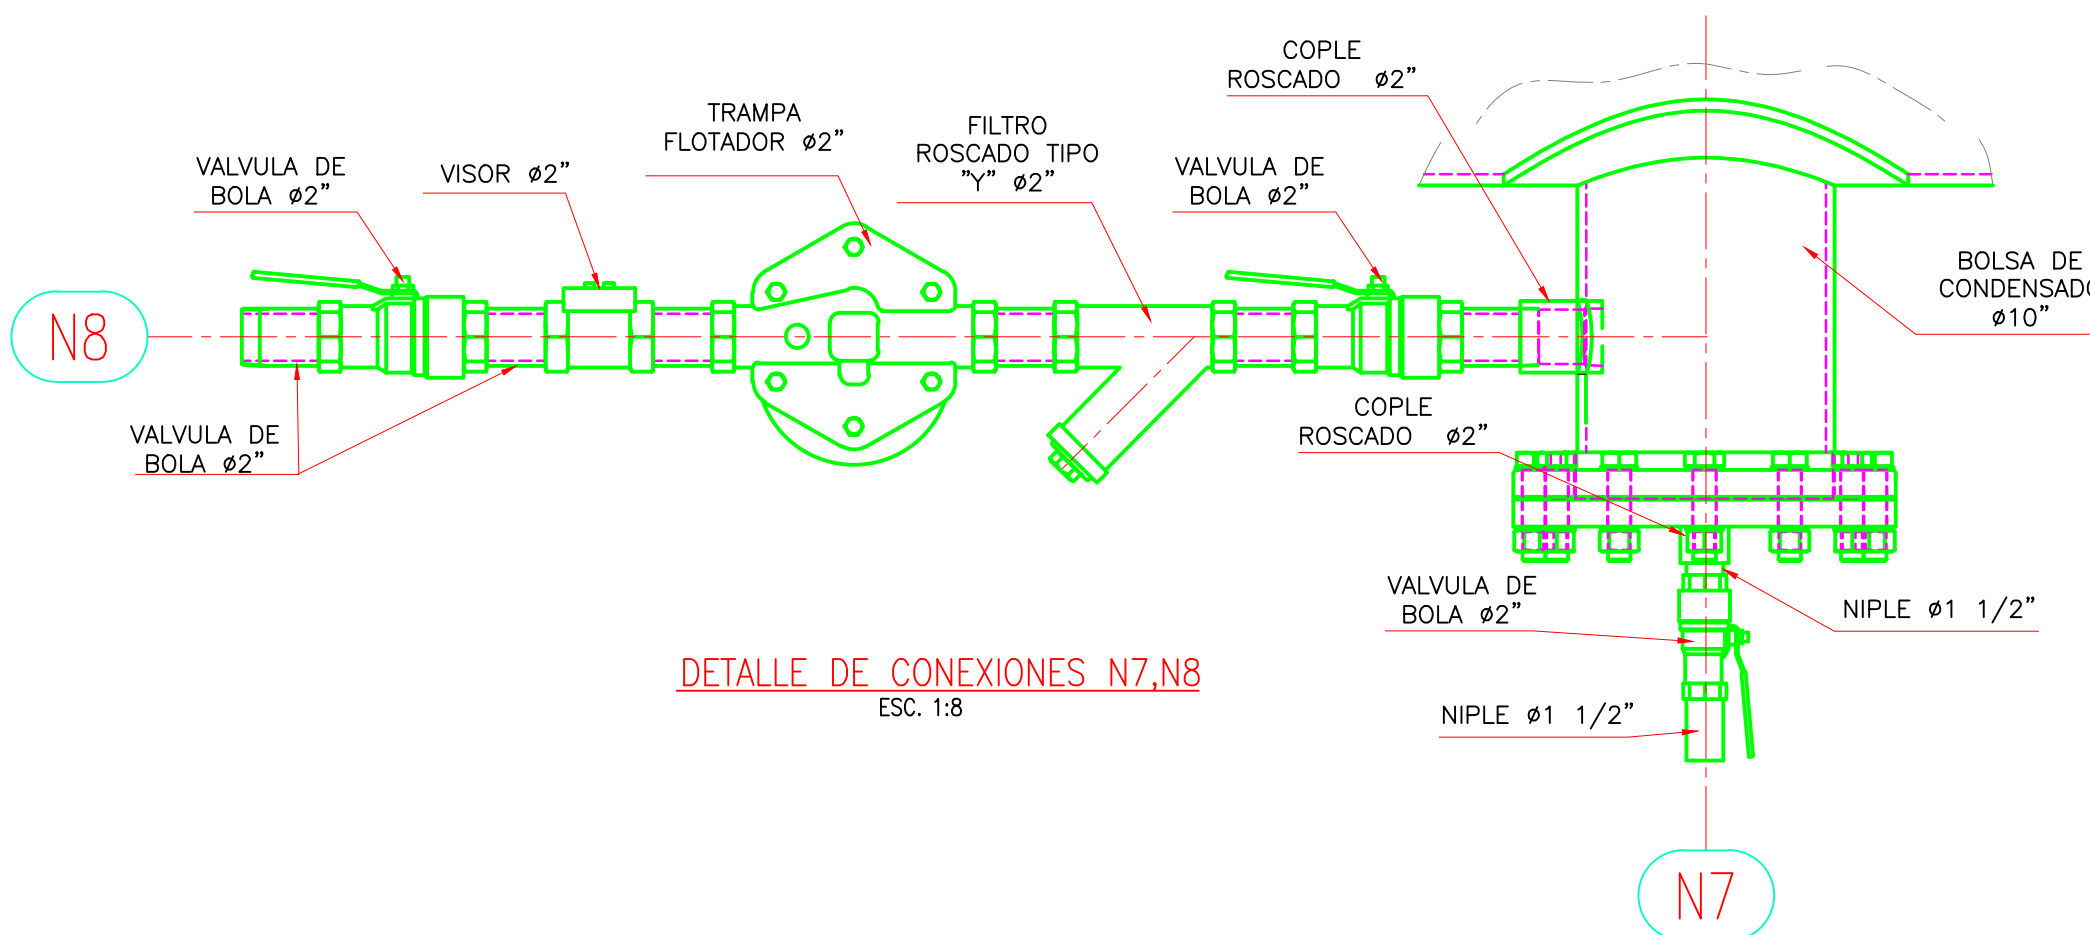

DETALLE DE CONEXIONES N7,N8
ESC. 1:8

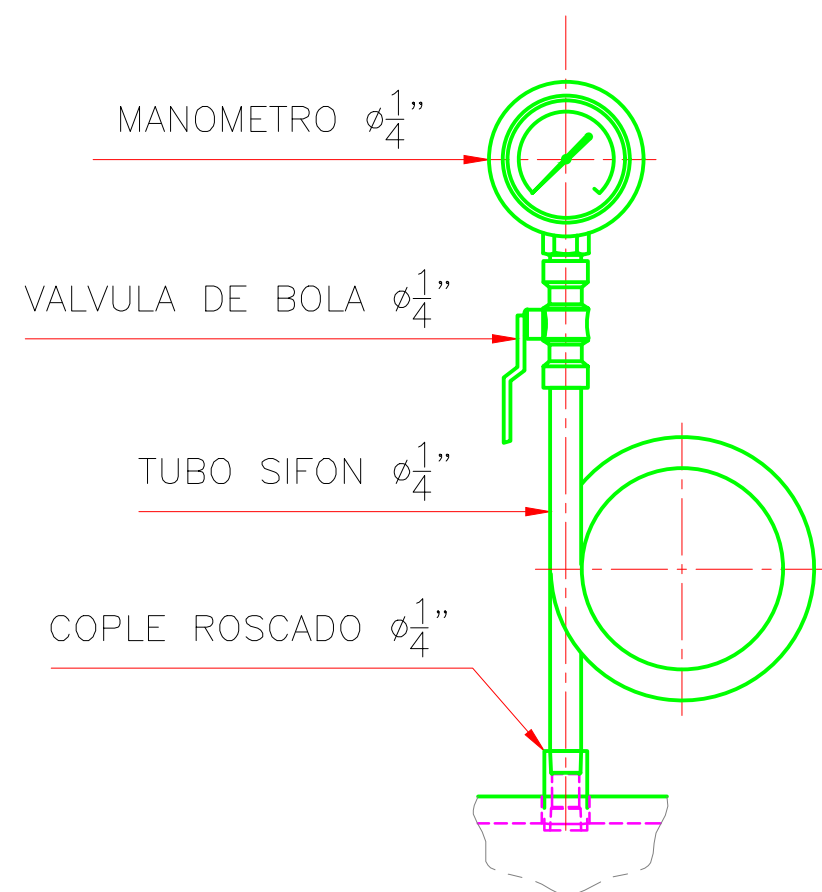

DETALLE DE CONEXION N1
ESC. 1:5

ACCESORIOS											
MARCA	CANT.	TAMAÑO	CLASE	CARA	CEDULA SCH.	TIPO	PROJ.	ALT.	ORIENT.	DESCRIPCION DEL SERVICIO	UBICACION
N1	01	ø 1/4"	-	-	-	-	-	-	-	-	-
N2	01	ø 12"	-	-	-	-	-	-	-	-	-
N3	01	ø 3"	-	-	-	-	-	-	-	-	-
N4	01	ø 16"	-	-	-	-	-	-	-	-	-
N5	01	ø 8"	-	-	-	-	-	-	-	-	-
N6	01	ø 12"	-	-	-	-	-	-	-	-	-
N7	01	ø 1 1/2"	-	-	-	-	-	-	-	-	-
N8	01	ø 2"	-	-	-	-	-	-	-	-	-